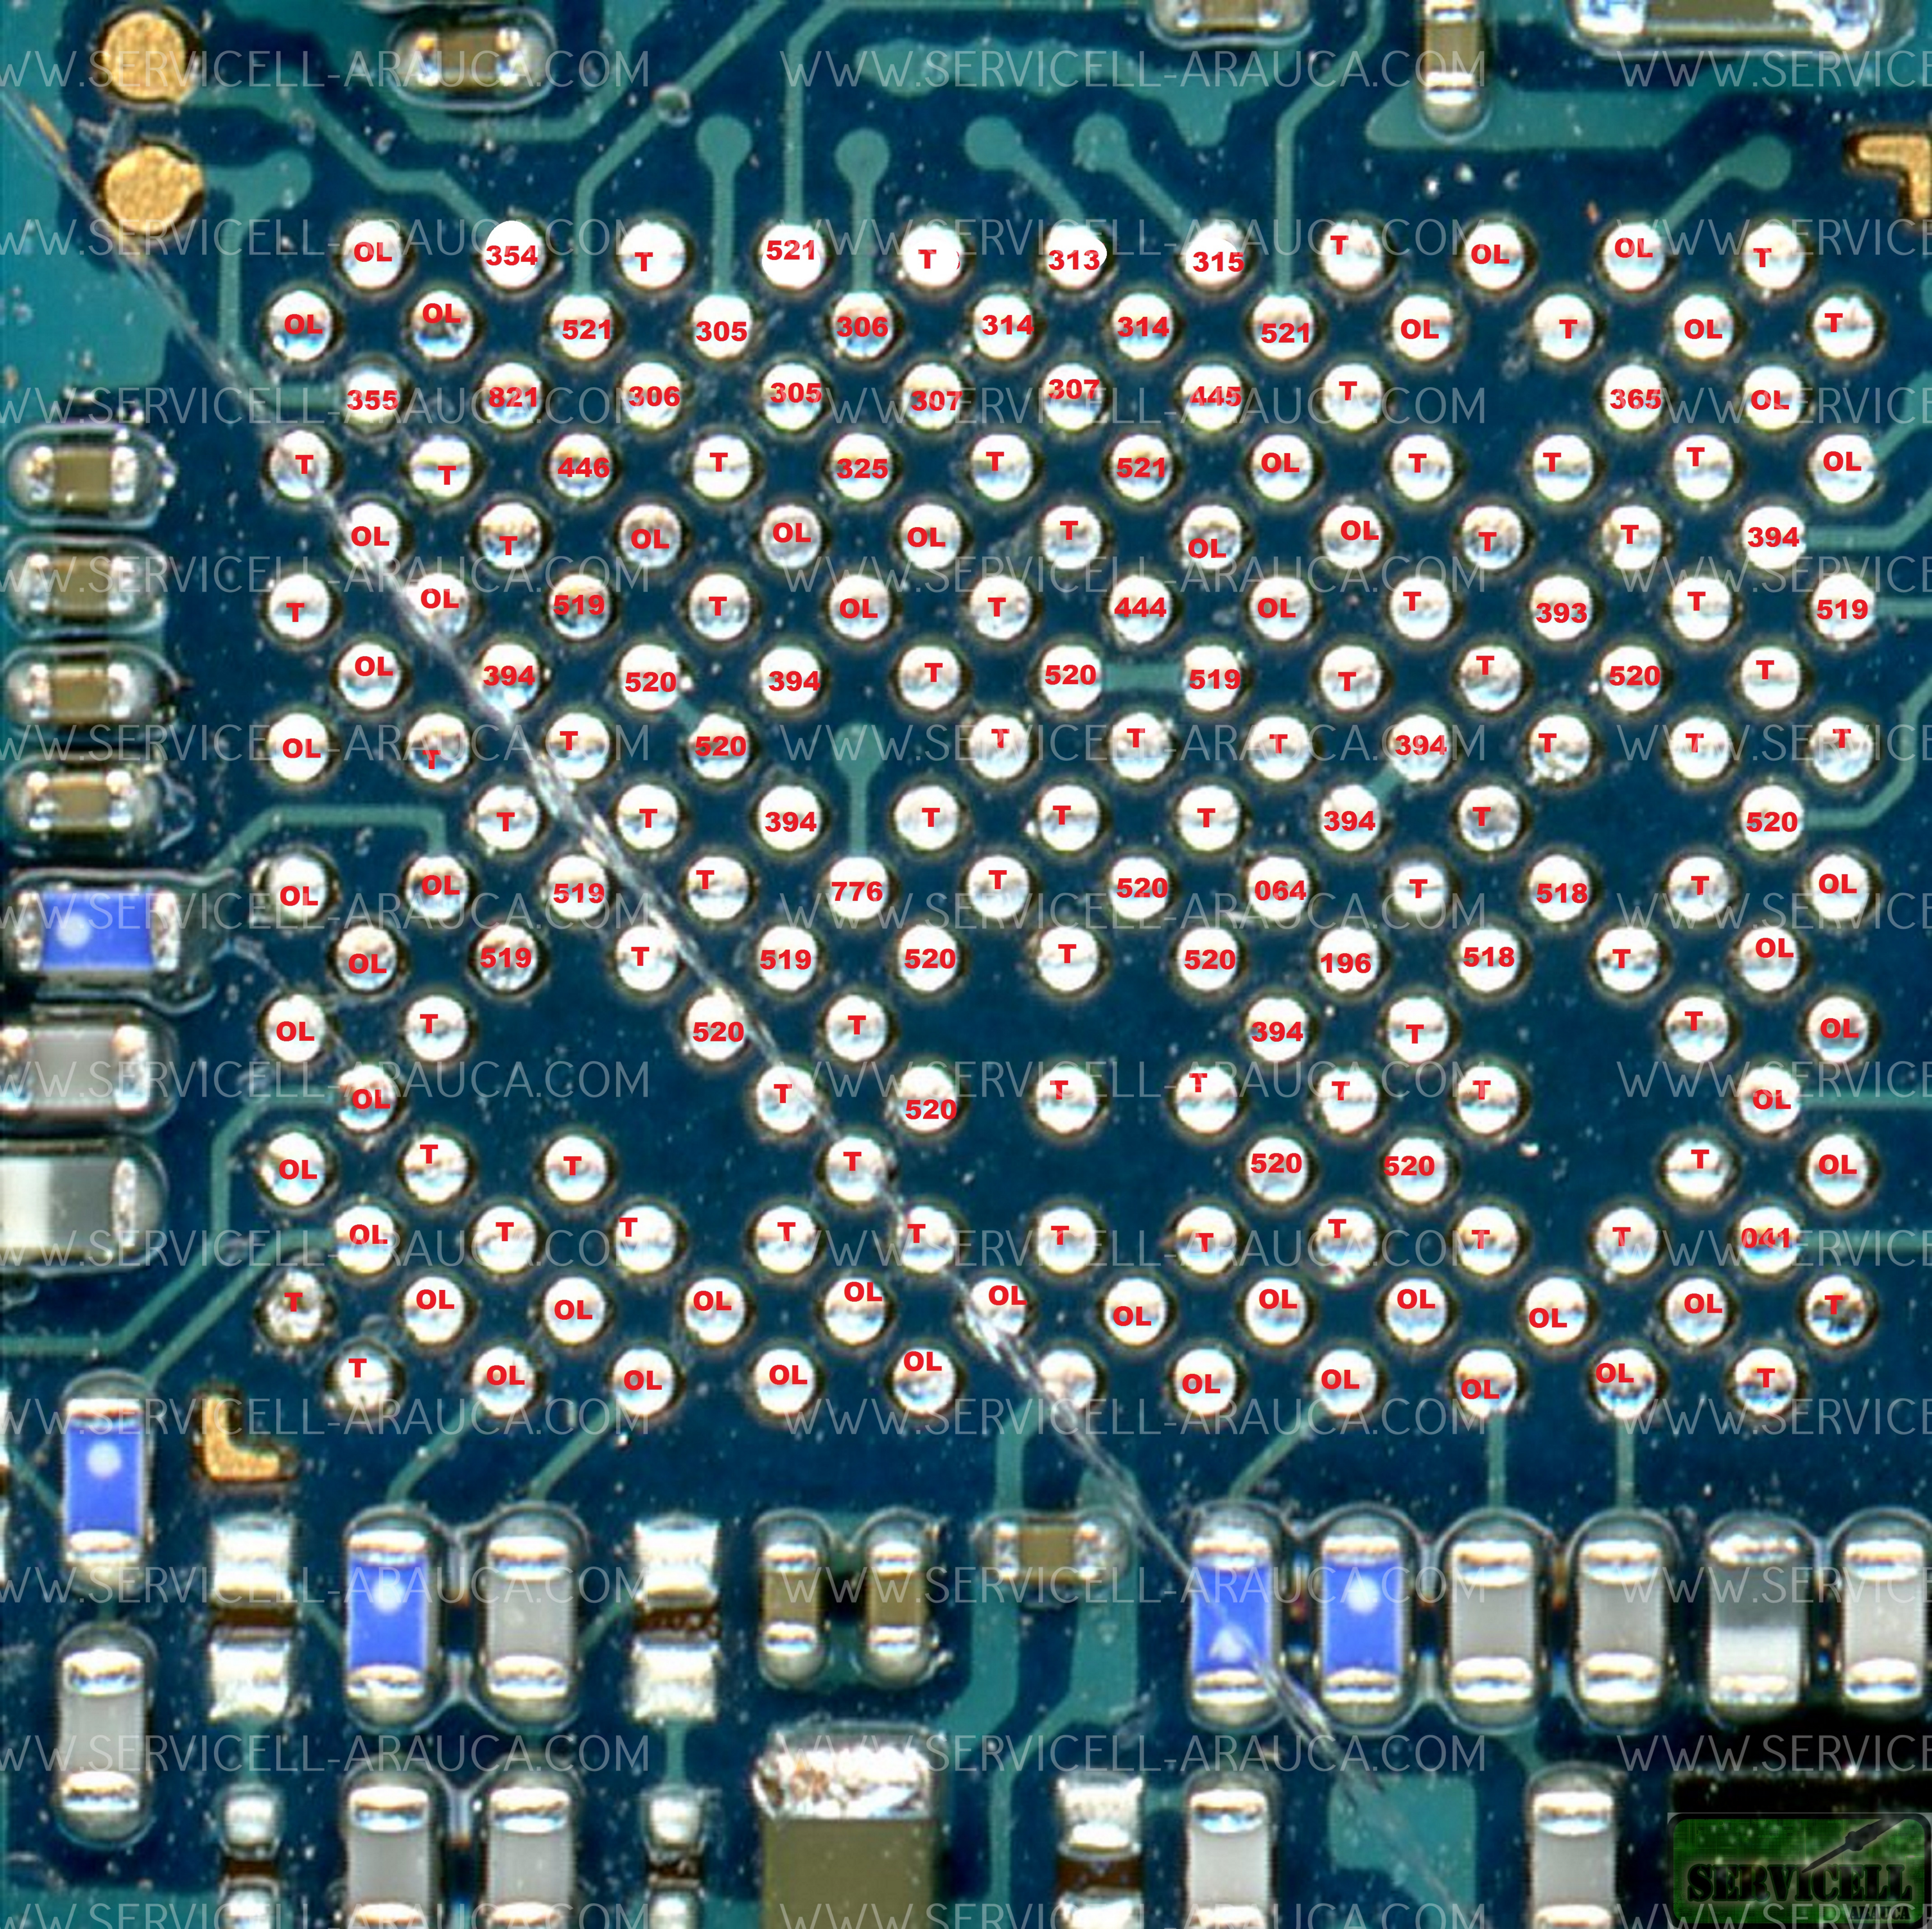
OL
354
T
521
T
313
315
T
OL
OL
T
OL
OL
521
305
306
314
314
521
OL
T
OL
T
355
821
306
305
307
307
445
T
365
OL
T
T
446
T
325
T
521
OL
T
T
T
OL
OL
T
OL
OL
OL
T
OL
OL
T
T
394
T
OL
519
T
OL
T
444
OL
T
393
T
519
OL
394
520
394
T
520
519
T
T
520
T
OL
T
T
520
T
T
T
394
T
T
T
T
T
394
T
T
T
394
T
520
OL
OL
519
T
776
T
520
064
T
518
T
OL
OL
519
T
519
520
T
520
196
518
T
OL
OL
T
520
T
394
T
T
OL
OL
T
520
T
T
T
T
OL
OL
T
T
T
520
520
T
OL
OL
T
T
T
T
T
T
T
T
T
041
T
OL
OL
OL
OL
OL
OL
OL
OL
OL
OL
T
T
OL
OL
OL
OL
OL
OL
OL
OL
T

WWW.SERVICELL-ARAUCA.COM