空点
接地
A15

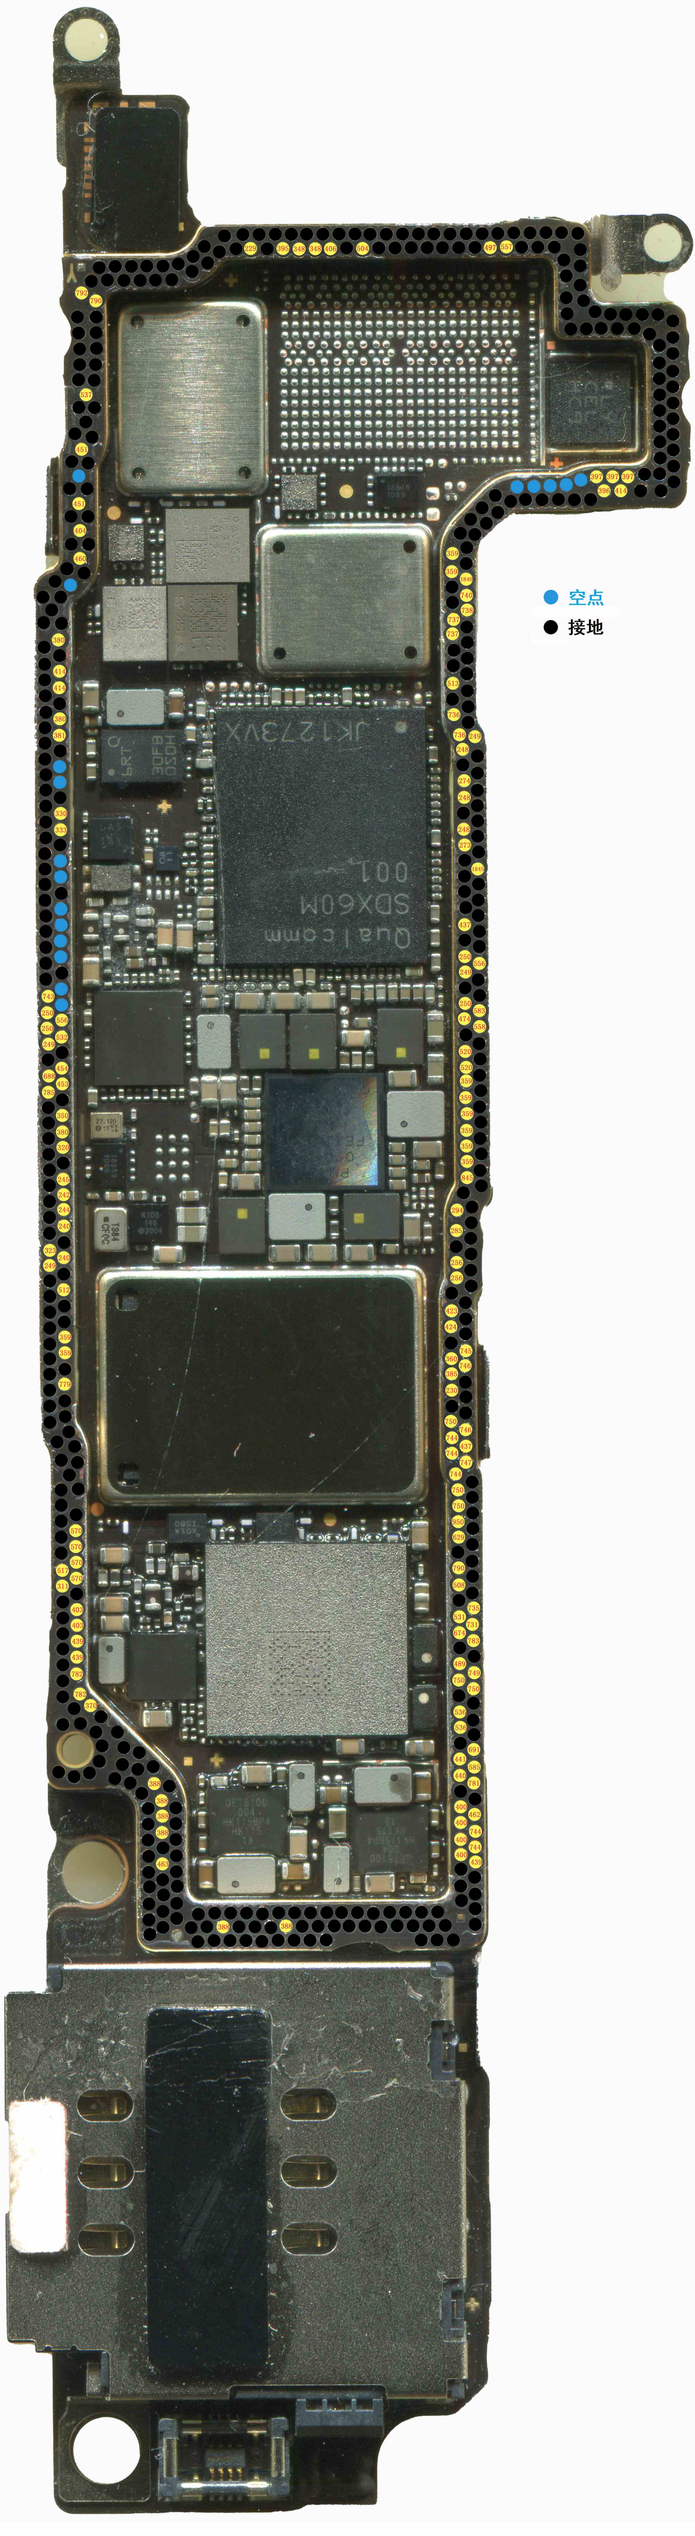
空点
接地