


REVISION RECORD			
LTR	ECO NO:	APPROVED:	DATE:

Project : MT6735 REF_SCH TOP LEVEL

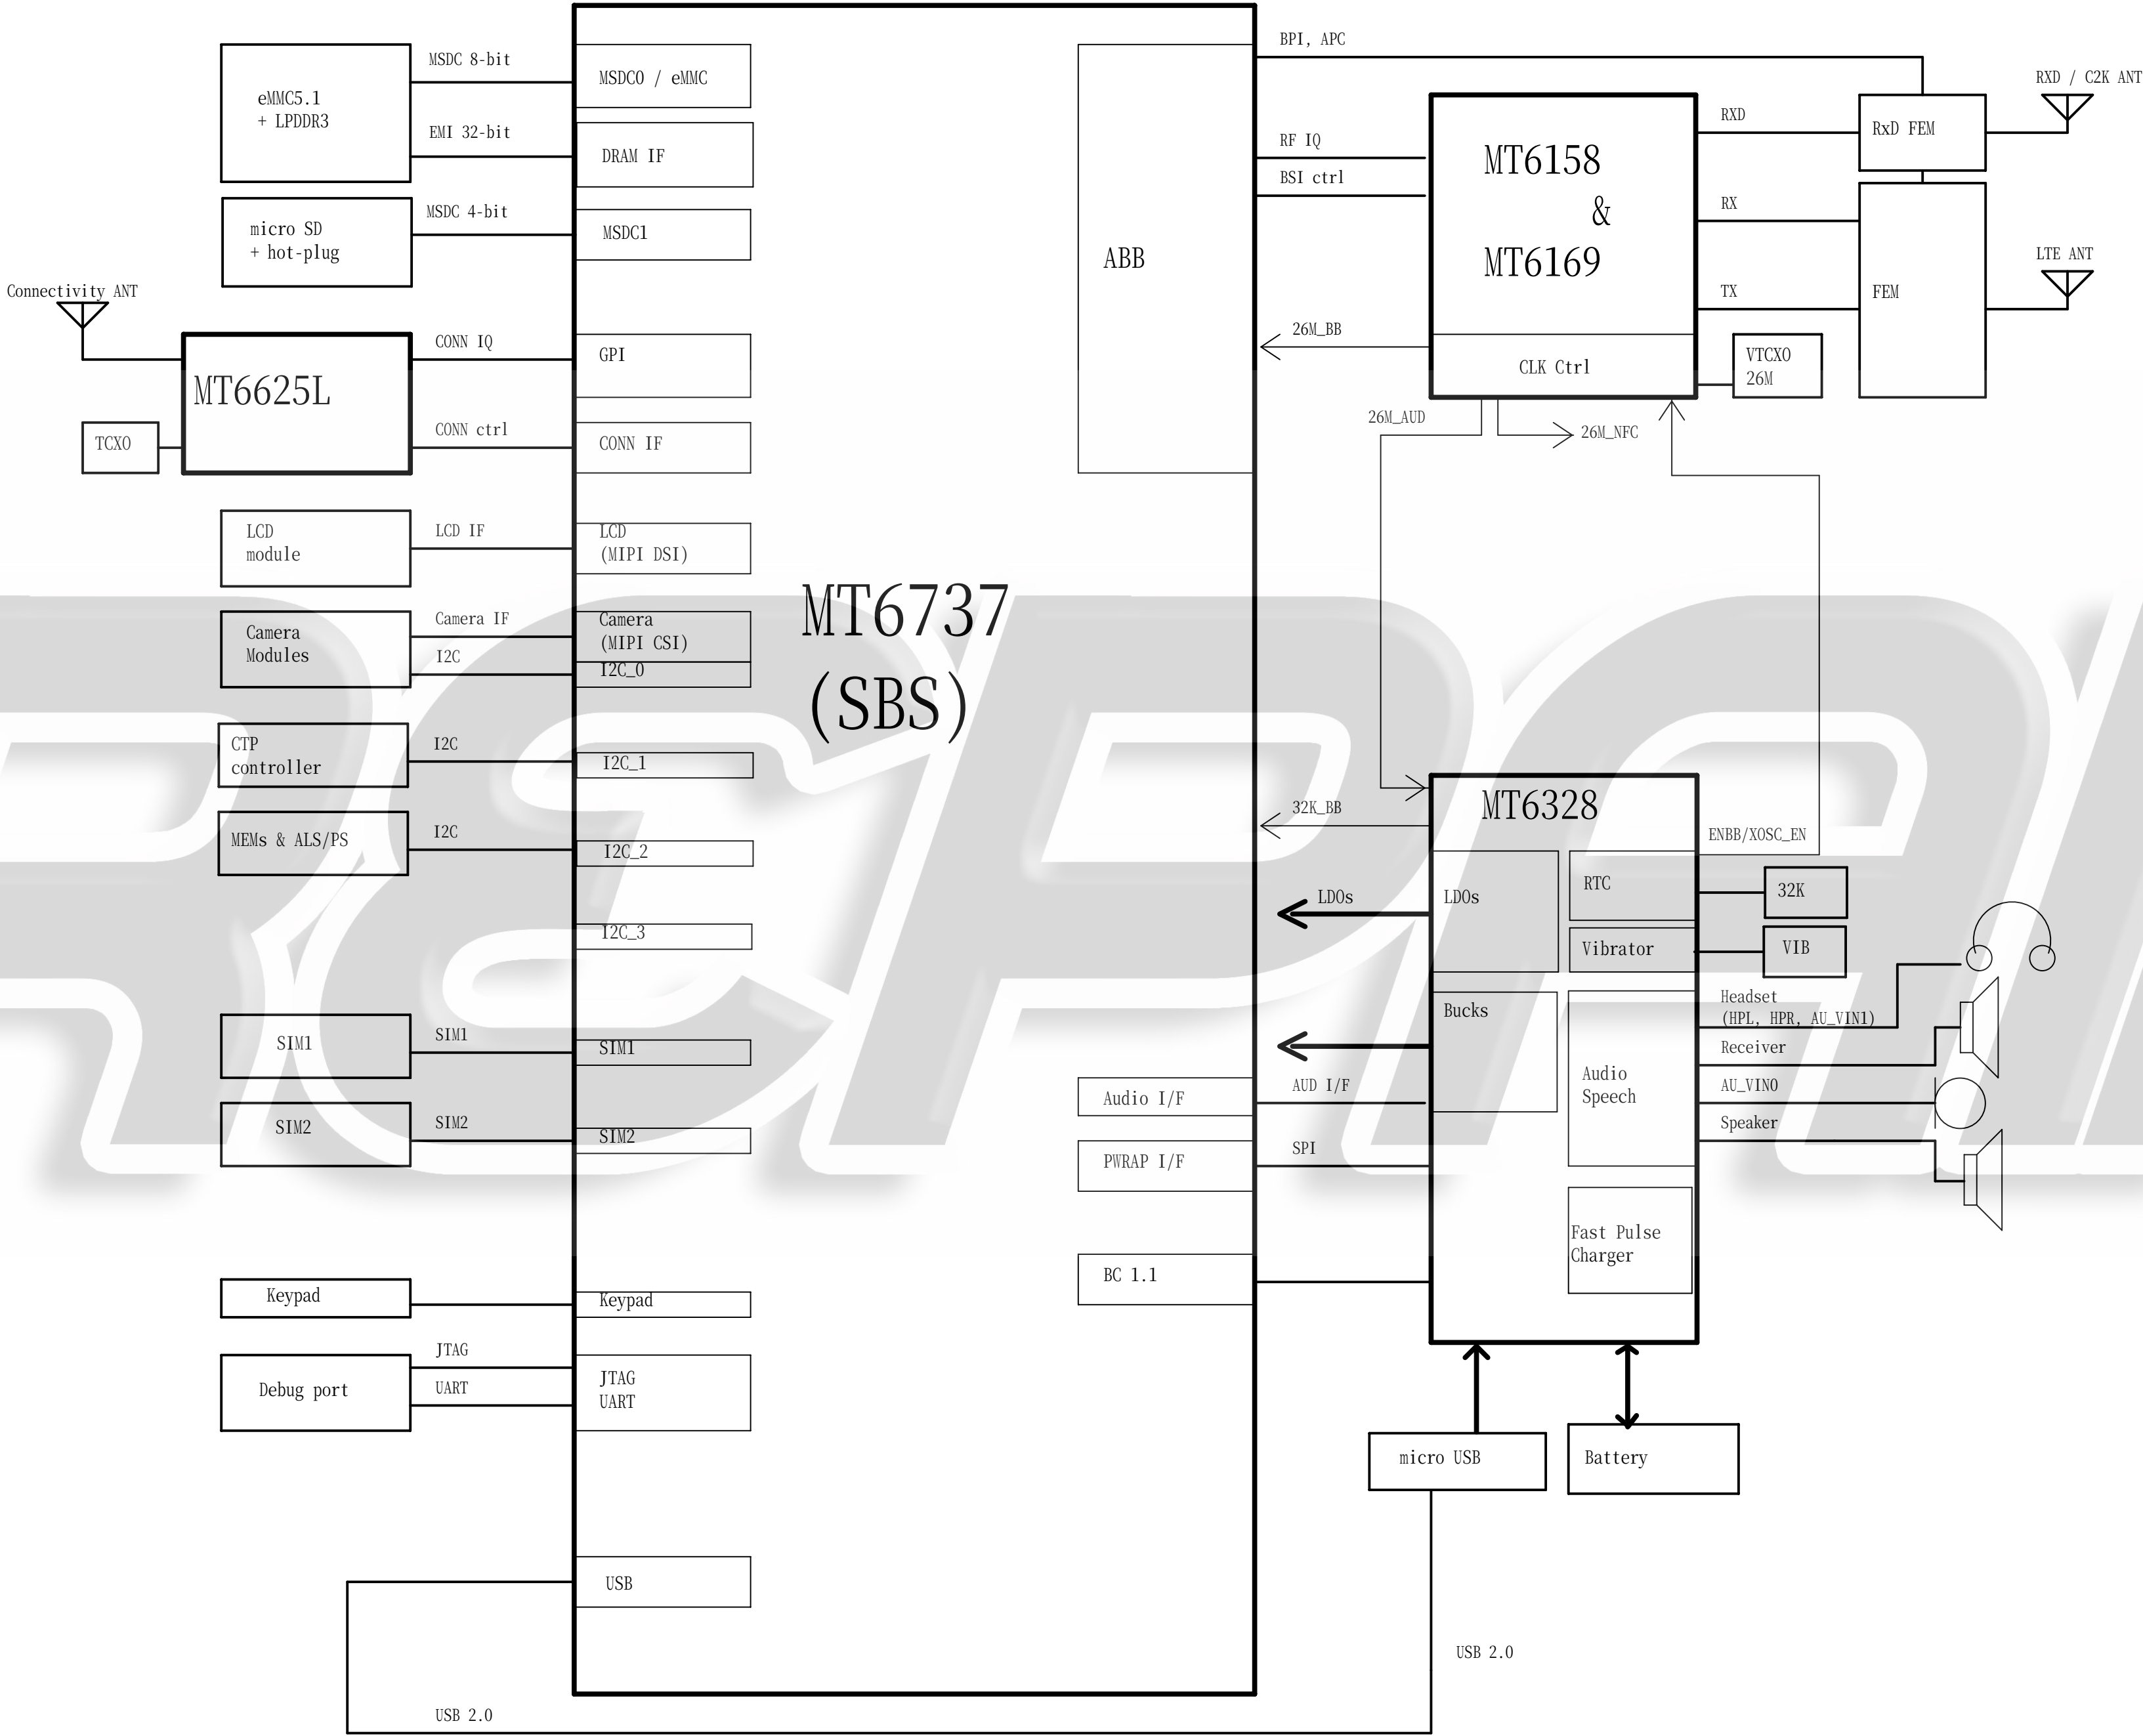

		COMPANY: WIND			
		TITLE: E187			
DRAWN: SUNHAO	DATED: 2016.01.21				
CHECKED: SUNHAO	DATED: <Checked Date>	CODE: <Code>	SIZE: D	DRAWING NO: <Drawing Number>	REV: <Revision>
QUALITY CONTROL: <QC By>	DATED: <QC Date>				
RELEASED: <Released By>	DATED: <Release Date>	SCALE: <Scale>			SHEET: 1 OF 23

REVISION RECORD			
LTR	ECO NO:	APPROVED:	DATE:


I2C	Function	I2C Spec.	Budget Timing	I2C Slave Address (7-bit mode)
I2C-0	Rear Camera - 8M	400 Kbps	Yes.	Rear camera (IMX219) I2C address: 0X10 (Write:0x20, Read:0x21) AF driver (DW9719S) I2C address: 0x0C (Write:0x18 , Read:0x19)
	Front Camera	400 Kbps	Yes.	Front camera (S5K5E8) I2C address: 0x2D (Write:0x5A, Read:0x5B)
I2C-1	CTP	400 Kbps	Yes.	S3603 / CTP I2C address: 0X20 (Write:0x40, Read:0x41)
I2C-2				
	Accelerometer	400 Kbps		BMA253 / Accelerometer I2C address: 0x3B (Write:0x76, Read:0x77)
	ALS / PS Sensor	400 Kbps		MN66238TKDN / ALS+PS I2C address: 0X49 (Write:0x92, Read:0x93)
	NFC	1.2 Mbps	Yes.	
I2C-3	Flashlight Driver	400 Kbps		

Note : I2C Spec. : Standard mode (100 kbps) and Fast mode (400 kbps), Fast mode Plus (1 Mbps) and High-speed mode (3.4 Mbps)



		COMPANY: WIND			
		TITLE: E187			
DRAWN: SUNHAO	DATED: 2016.01.21				
CHECKED: SUNHAO	DATED: <Checked Date>	CODE:	SIZE:	DRAWING NO:	REV:
QUALITY CONTROL: <QC By>	DATED: <QC Date>	<Code>	D	<Drawing Number>	<Revision>
RELEASED: <Released By>	DATED: <Release Date>	SCALE: <Scale>			SHEET: 2 of 23





REVISION RECORD			
LTR	ECO NO:	APPROVED:	DATE:

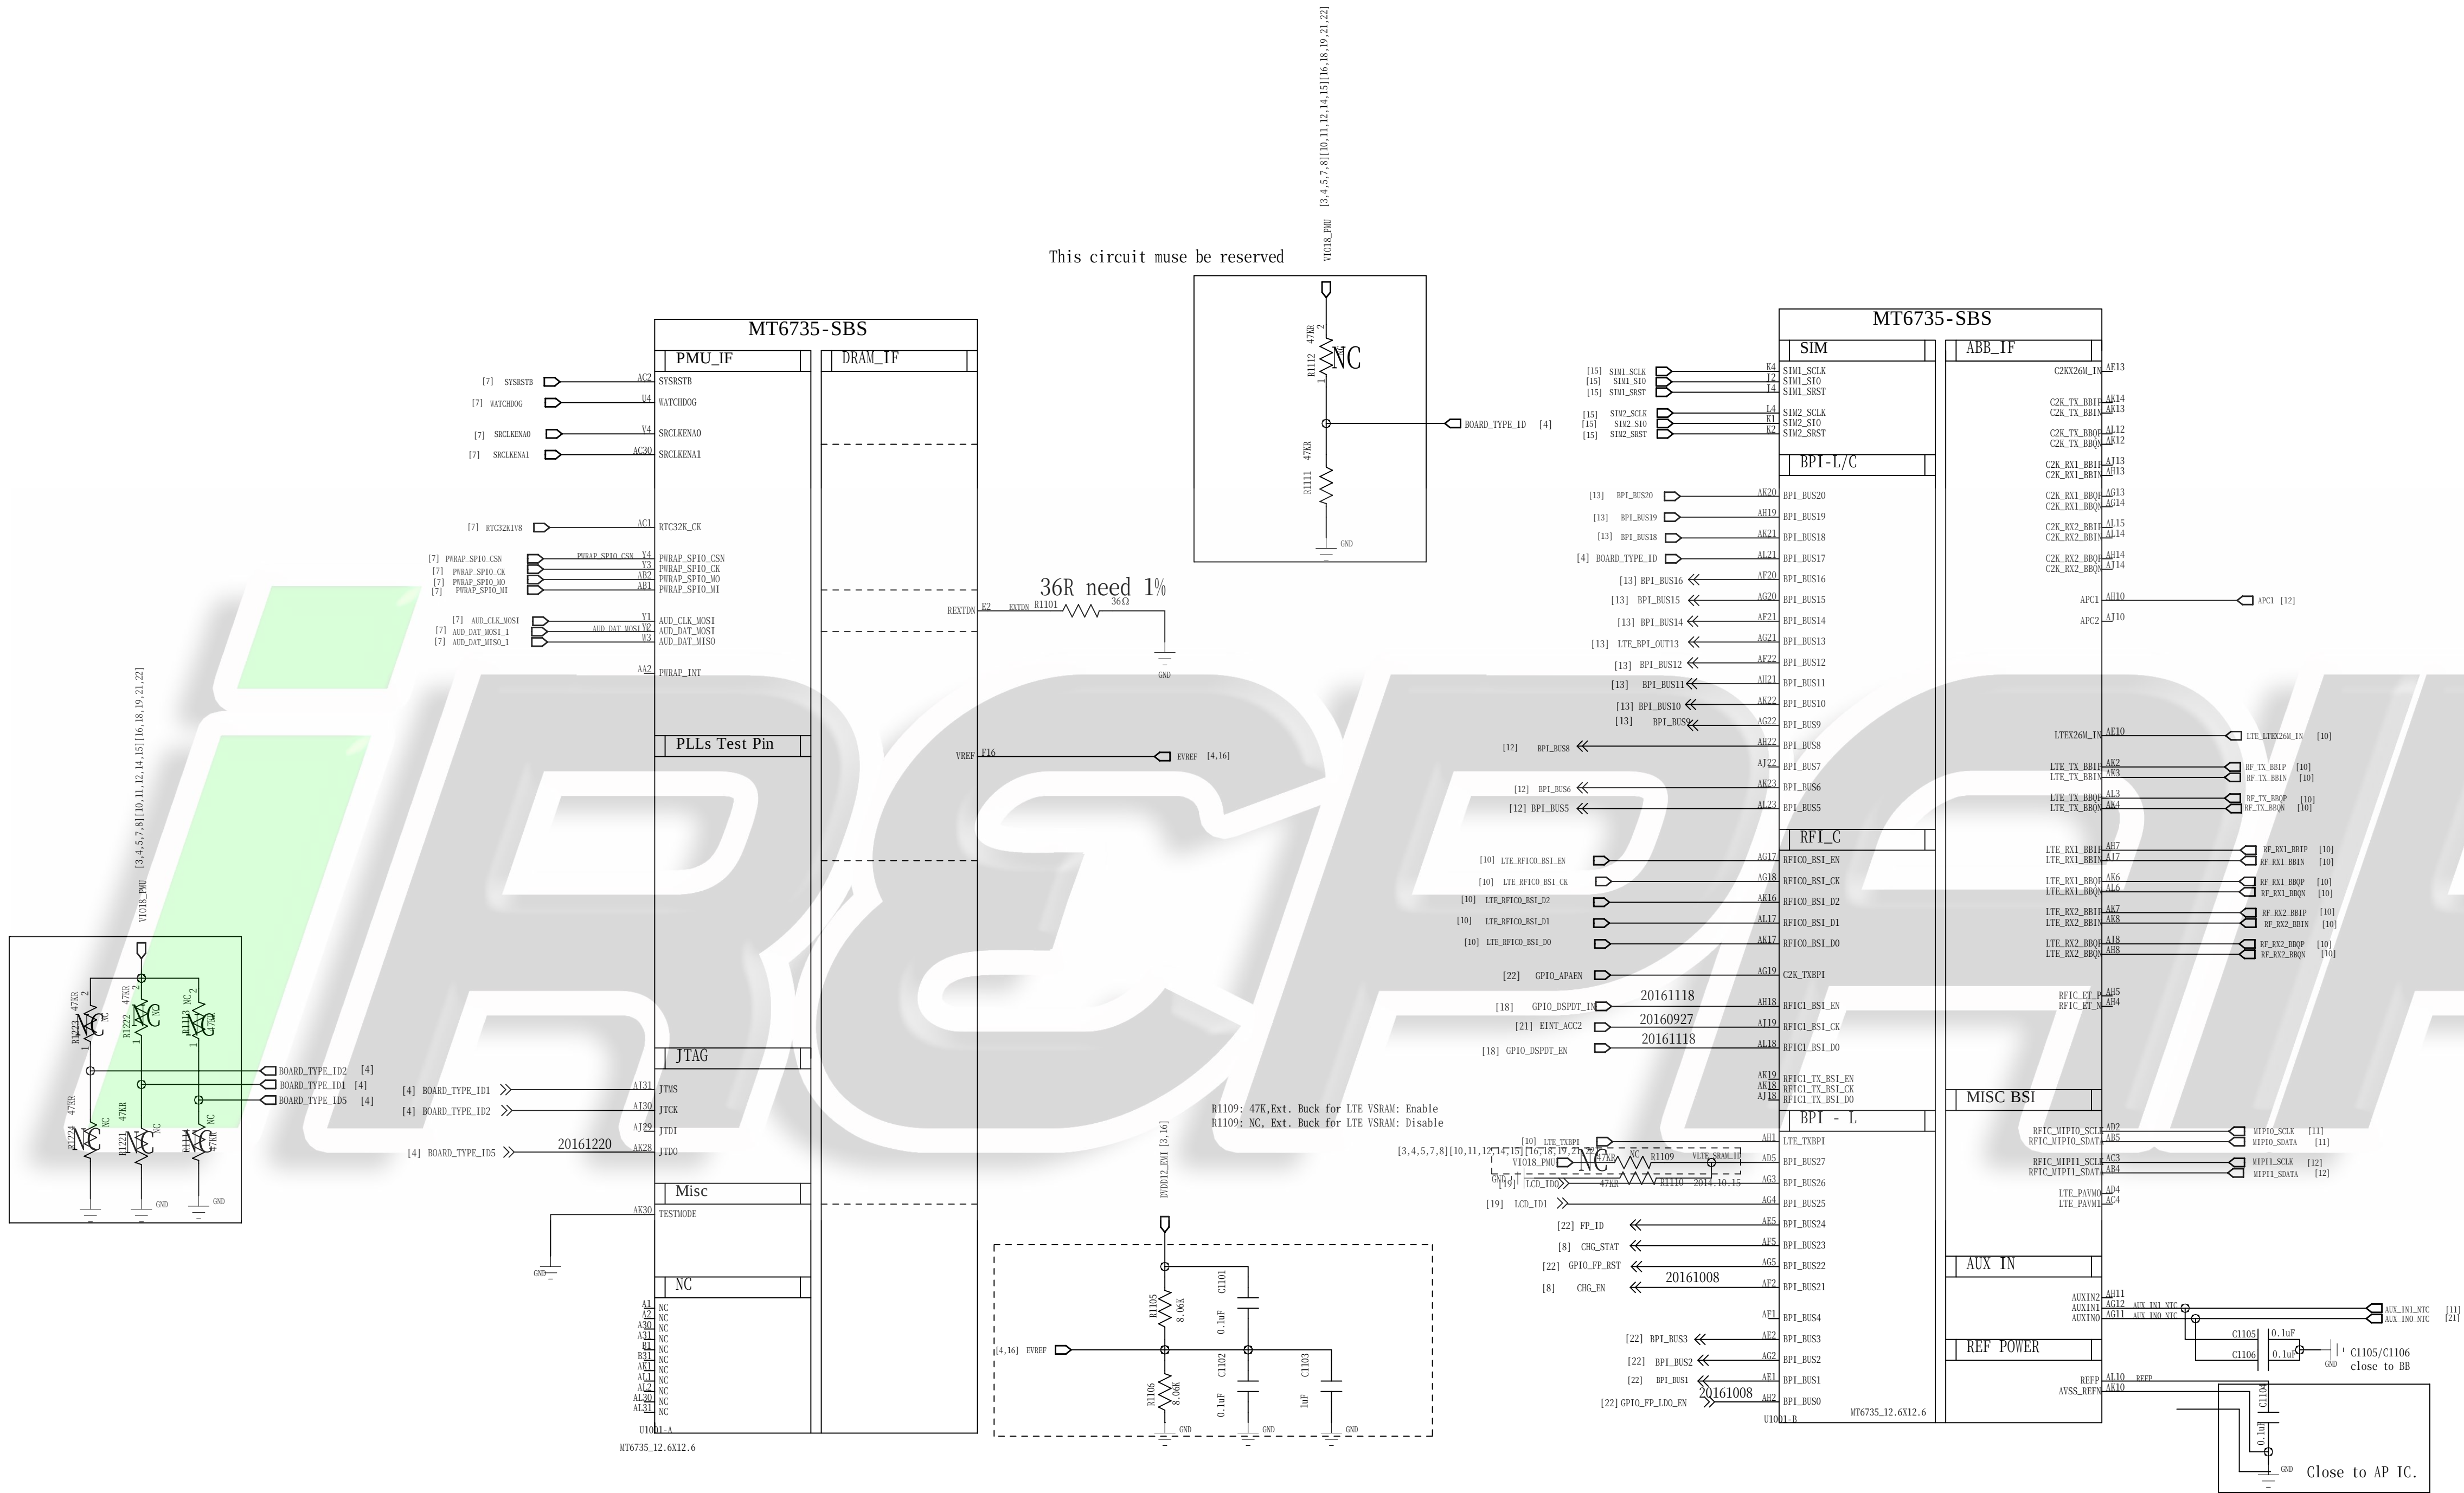

DRAWN:	SUNHAO	DATED:	2016.01.21
CHECKED:		DATED:	
QUALITY CONTROL:		DATED:	
RELEASED:		DATED:	



COMPANY: WIND			
TITLE: E187			
CODE:	SIZE:	DRAFTING NO:	REV:
SCALE:		SHEET: 4 of 23	

REVISION RECORD			
LTR	ECO NO:	APPROVED:	DATE:

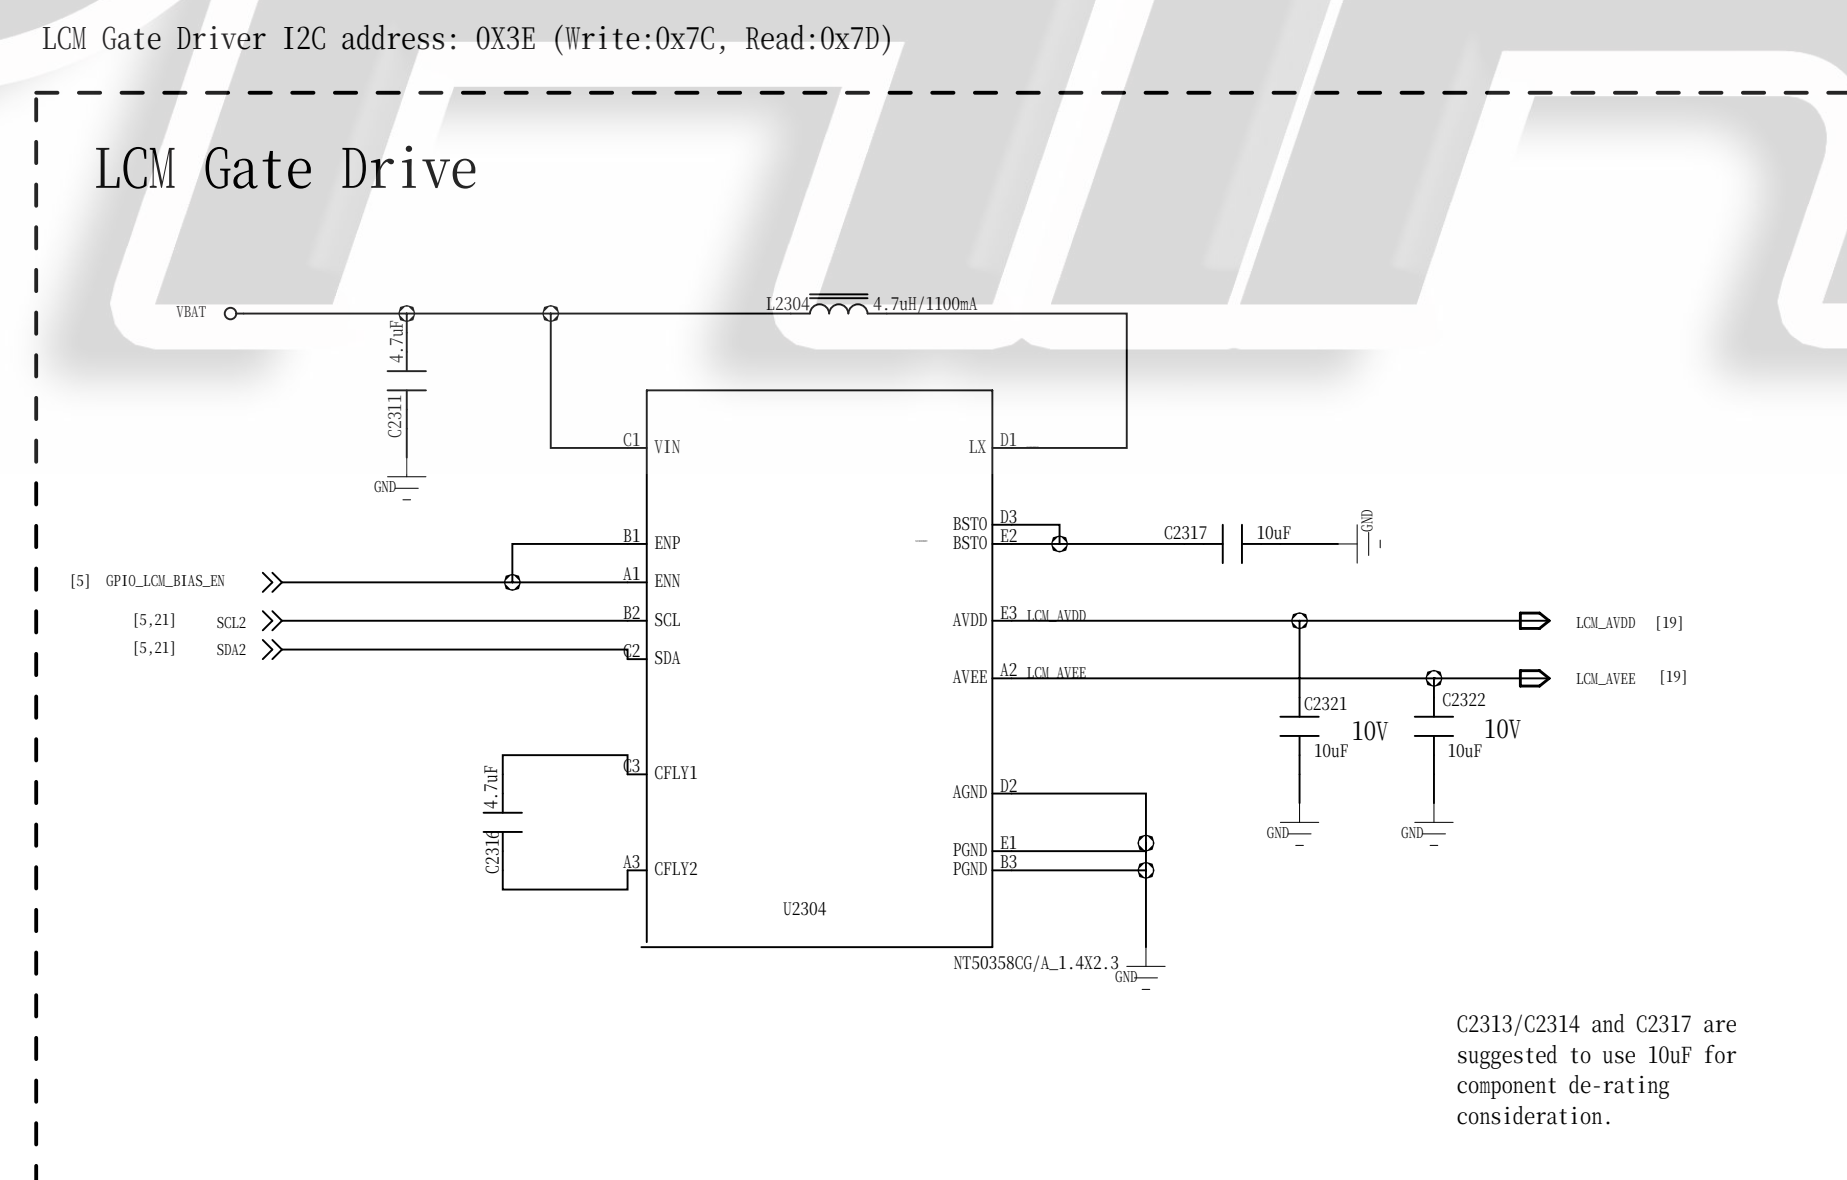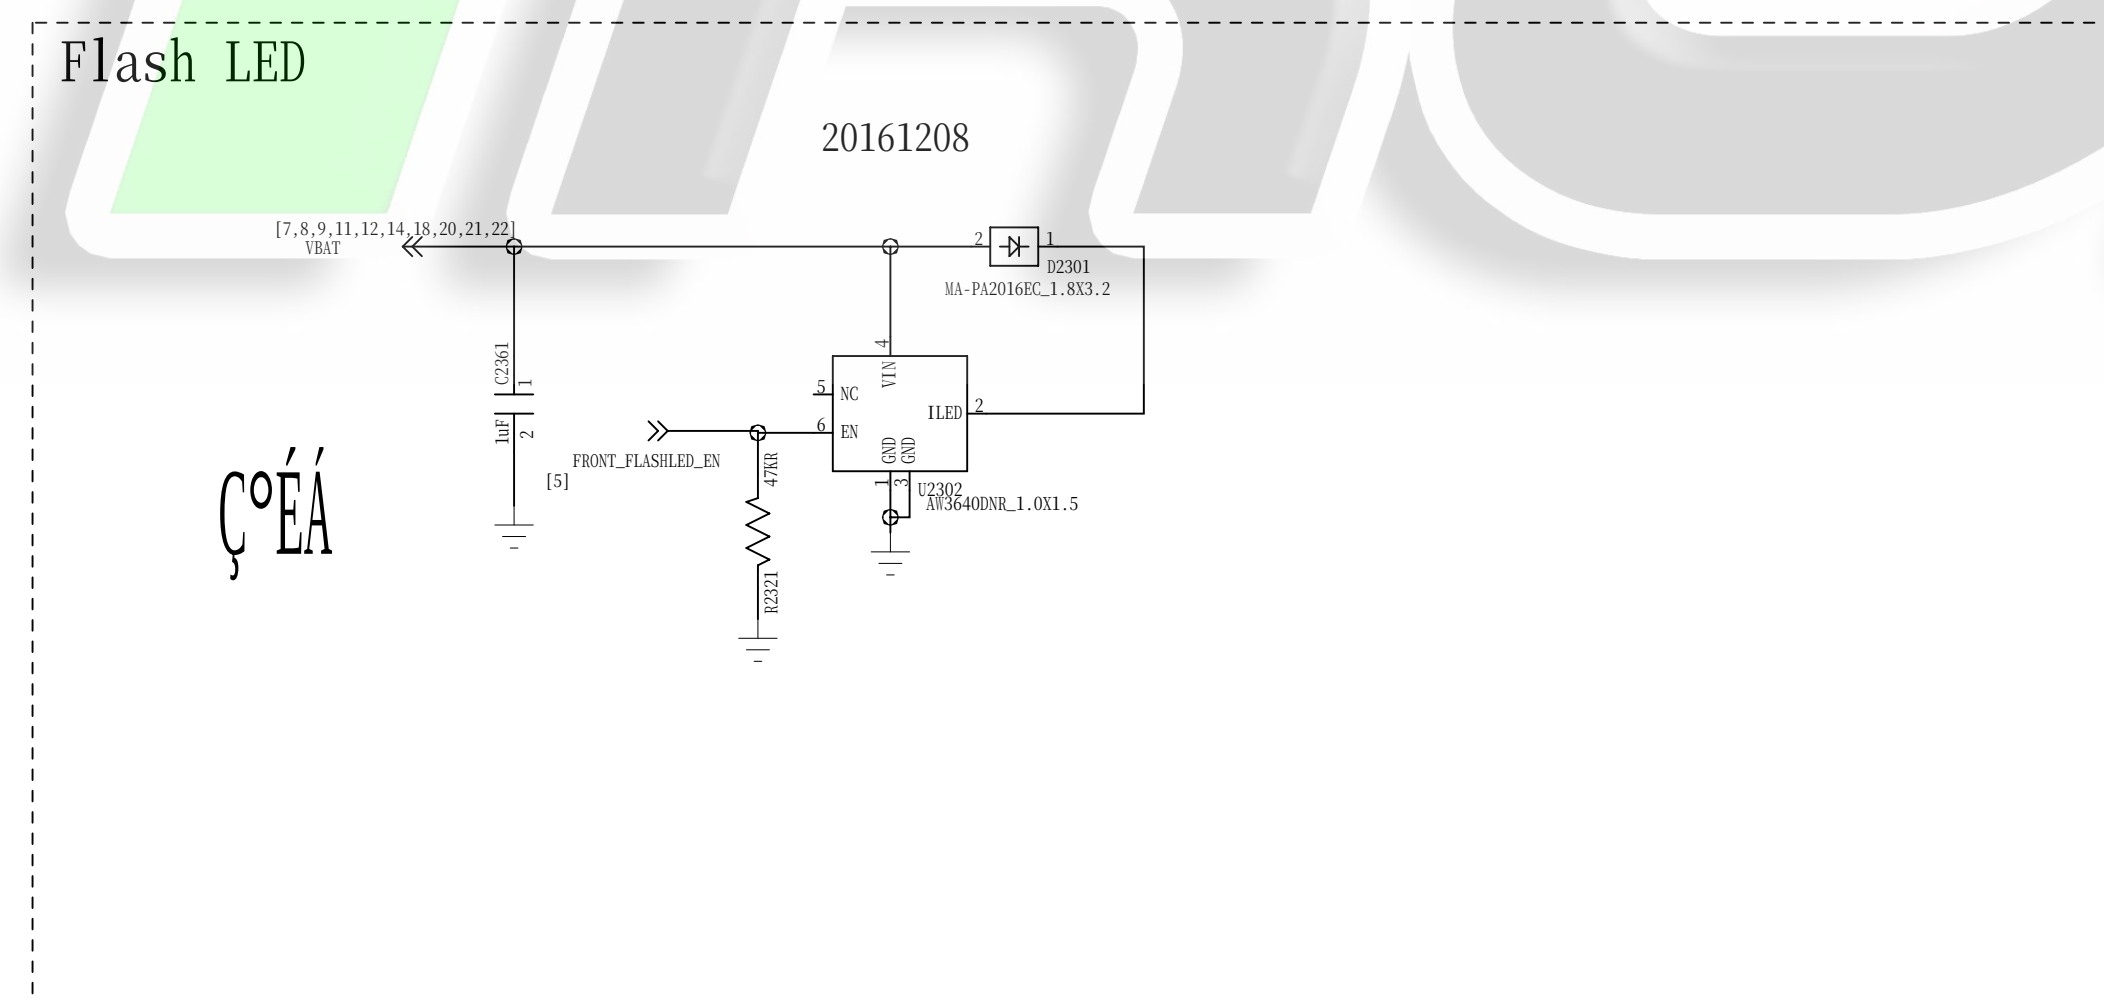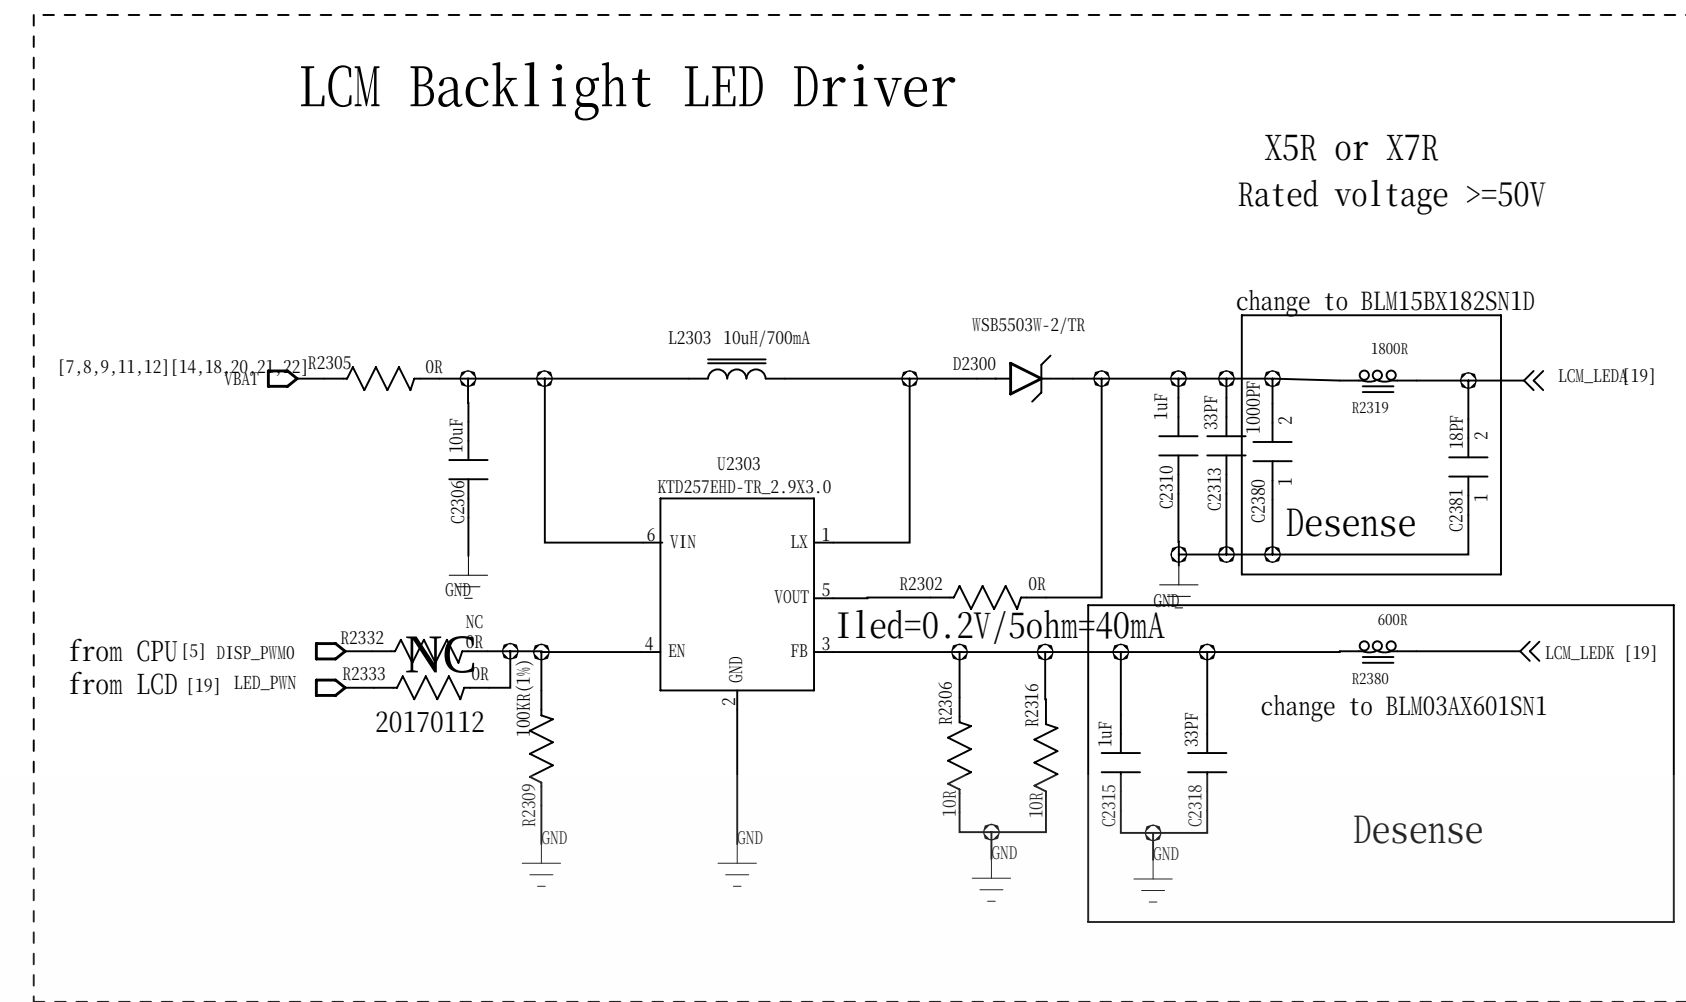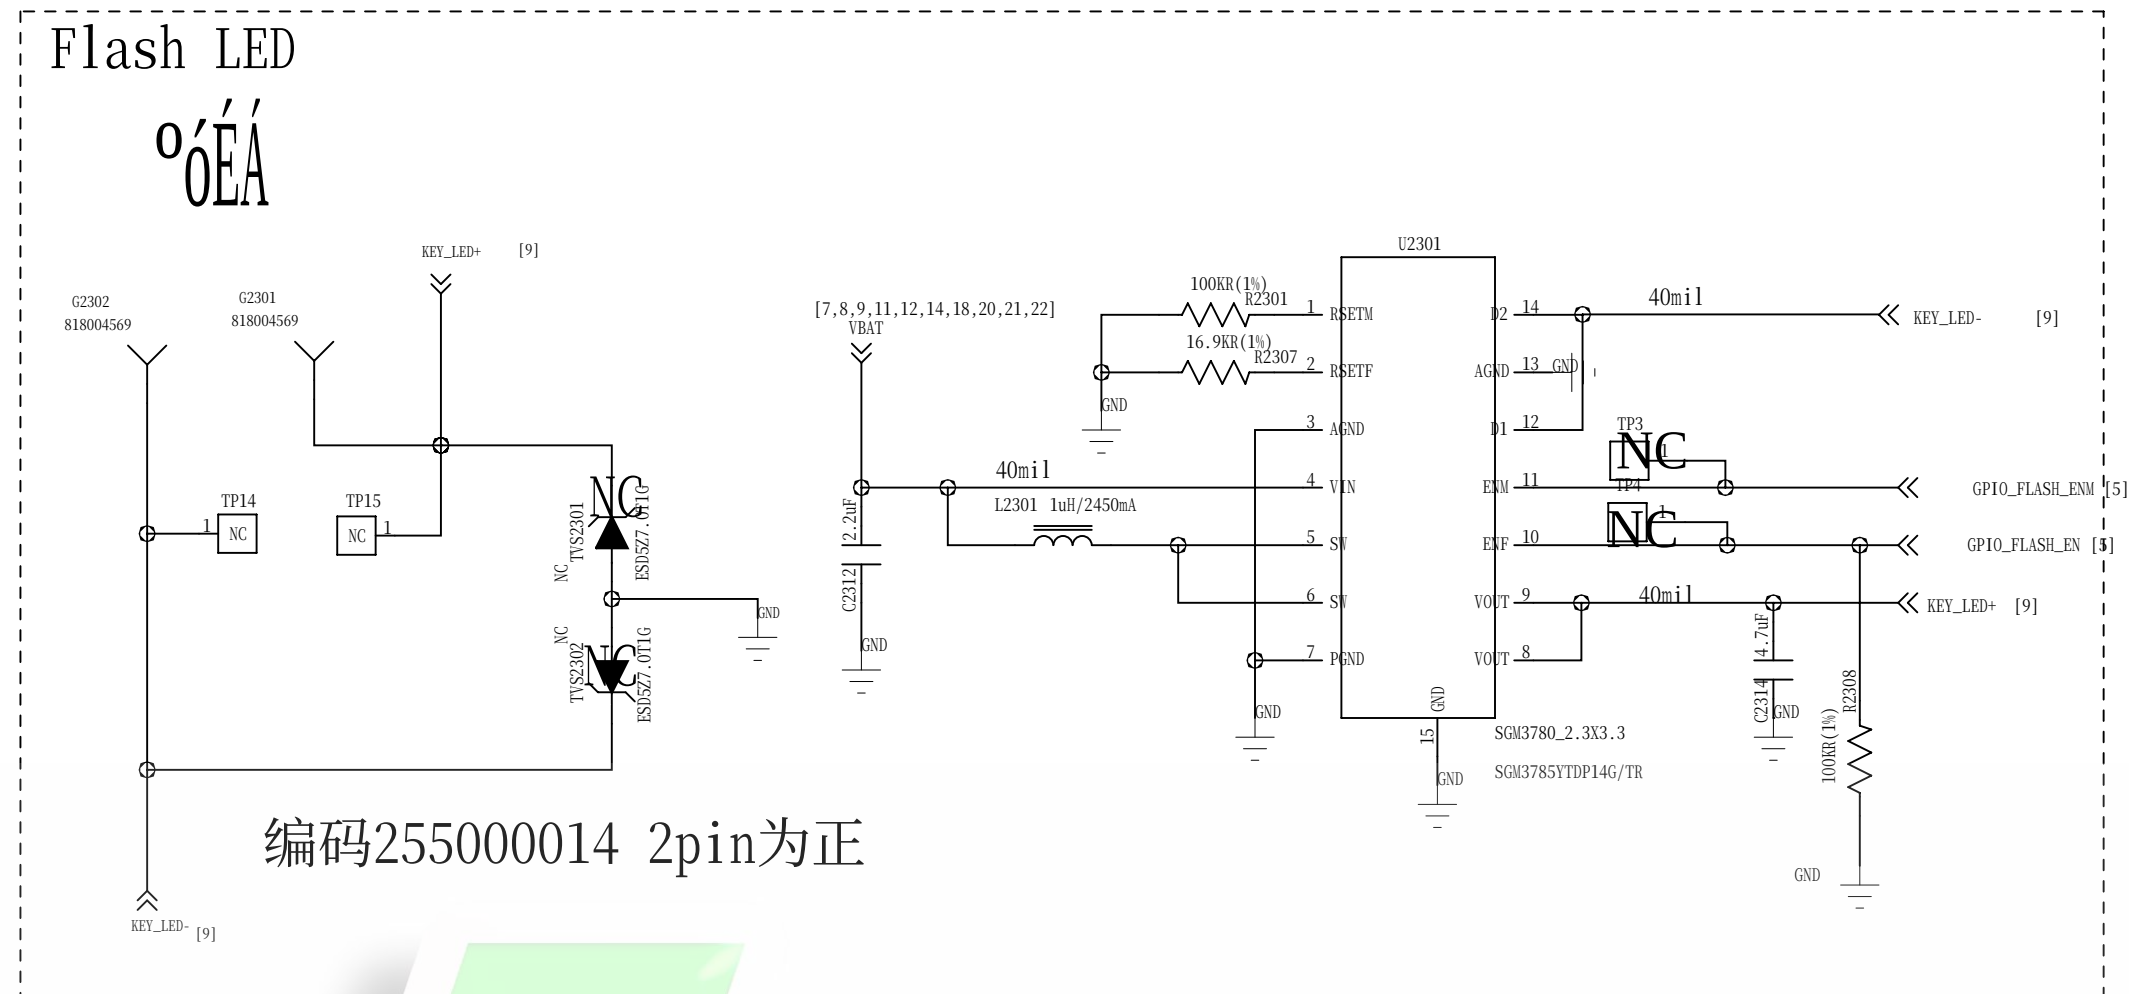

have checked

DRAWN: SUNHAO		DATE: 2016.01.21		COMPANY: WIND			
				TITLE: E187			
CHECKED:	DATE:	CODE:	SIZE:	DRAWING NO:			REV:
QUALITY CONTROL:	DATE:						
RELEASED:	DATE:	SCALE: <Scale>			SHEET: 9 OF 23		
<Released By>	<Release Date>						

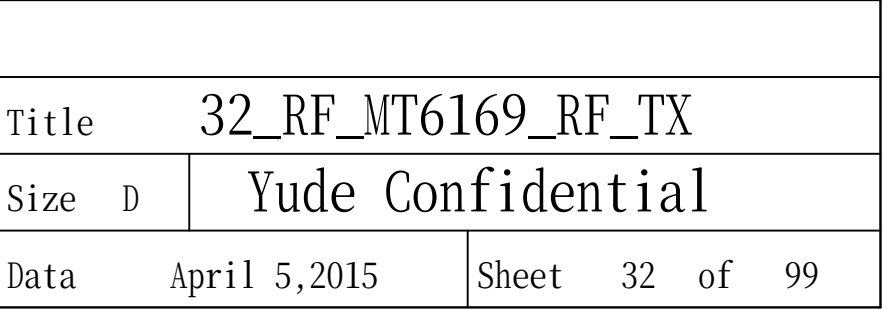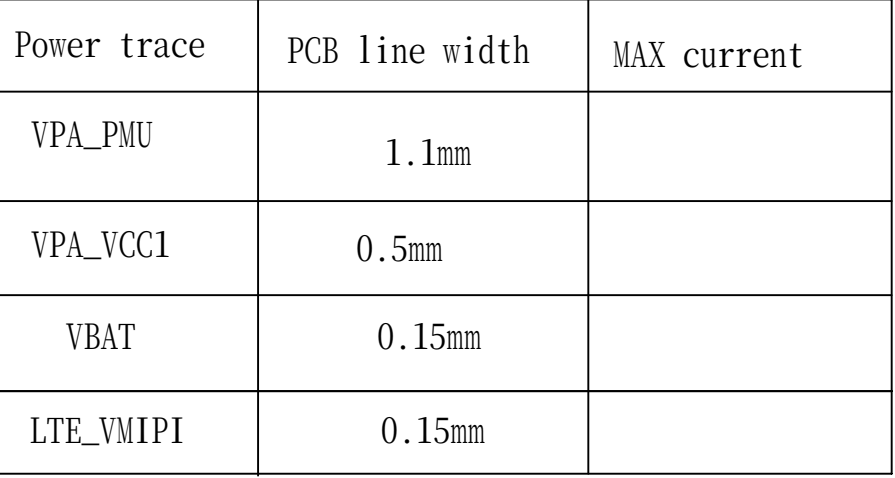

REVISION RECORD			
LTR	ECO NO:	APPROVED:	DATE:

Connect to AP			
DQ[0..31]	DQ[0..31]		
CA[0..9]	CA[0..9]		
CS0_N	CS0_N		
CS1_N	CS1_N		
CKE	CKE		
DQM0	DQM0		
DQM1	DQM1		
DQM2	DQM2		
DQM3	DQM3		
DQS0_C	DQS0_C		
DQS1_C	DQS1_C		
DQS2_C	DQS2_C		
DQS3_C	DQS3_C		
DQS0_T	DQS0_T		
DQS1_T	DQS1_T		
DQS2_T	DQS2_T		
DQS3_T	DQS3_T		
CLK0_T	CLK0_T		
CLK0_C	CLK0_C		
VREF_CA	VREF_CA		
VREF_DQ	VREF_DQ		
MSDCO_RSTB	MSDCO_RSTB		
MSDCO_CMD	MSDCO_CMD		
MSDCO_CLK	MSDCO_CLK		
MSDCO_DSL	MSDCO_DSL		
MSDCO_DAT0	MSDCO_DAT0		
MSDCO_DAT1	MSDCO_DAT1		
MSDCO_DAT2	MSDCO_DAT2		
MSDCO_DAT3	MSDCO_DAT3		
MSDCO_DAT4	MSDCO_DAT4		
MSDCO_DAT5	MSDCO_DAT5		
MSDCO_DAT6	MSDCO_DAT6		
MSDCO_DAT7	MSDCO_DAT7		
Power I/F			
VIO18_PMU	VIO18_PMU		
VEMC_3V3_PMU	VEMC_3V3_PMU		
DVDD12_EM1	DVDD12_EM1		

eMMC+LPDDR3

221 Ball, 0.5mm pitch

VDD1=1.8V


VDD2=1.20V


VDDCA=1.2V

VDDQ= 1.20V

8GB eMMC + 8Gb LPDDR3


Hynix/H9TQ64A8GTMCUR-KUM

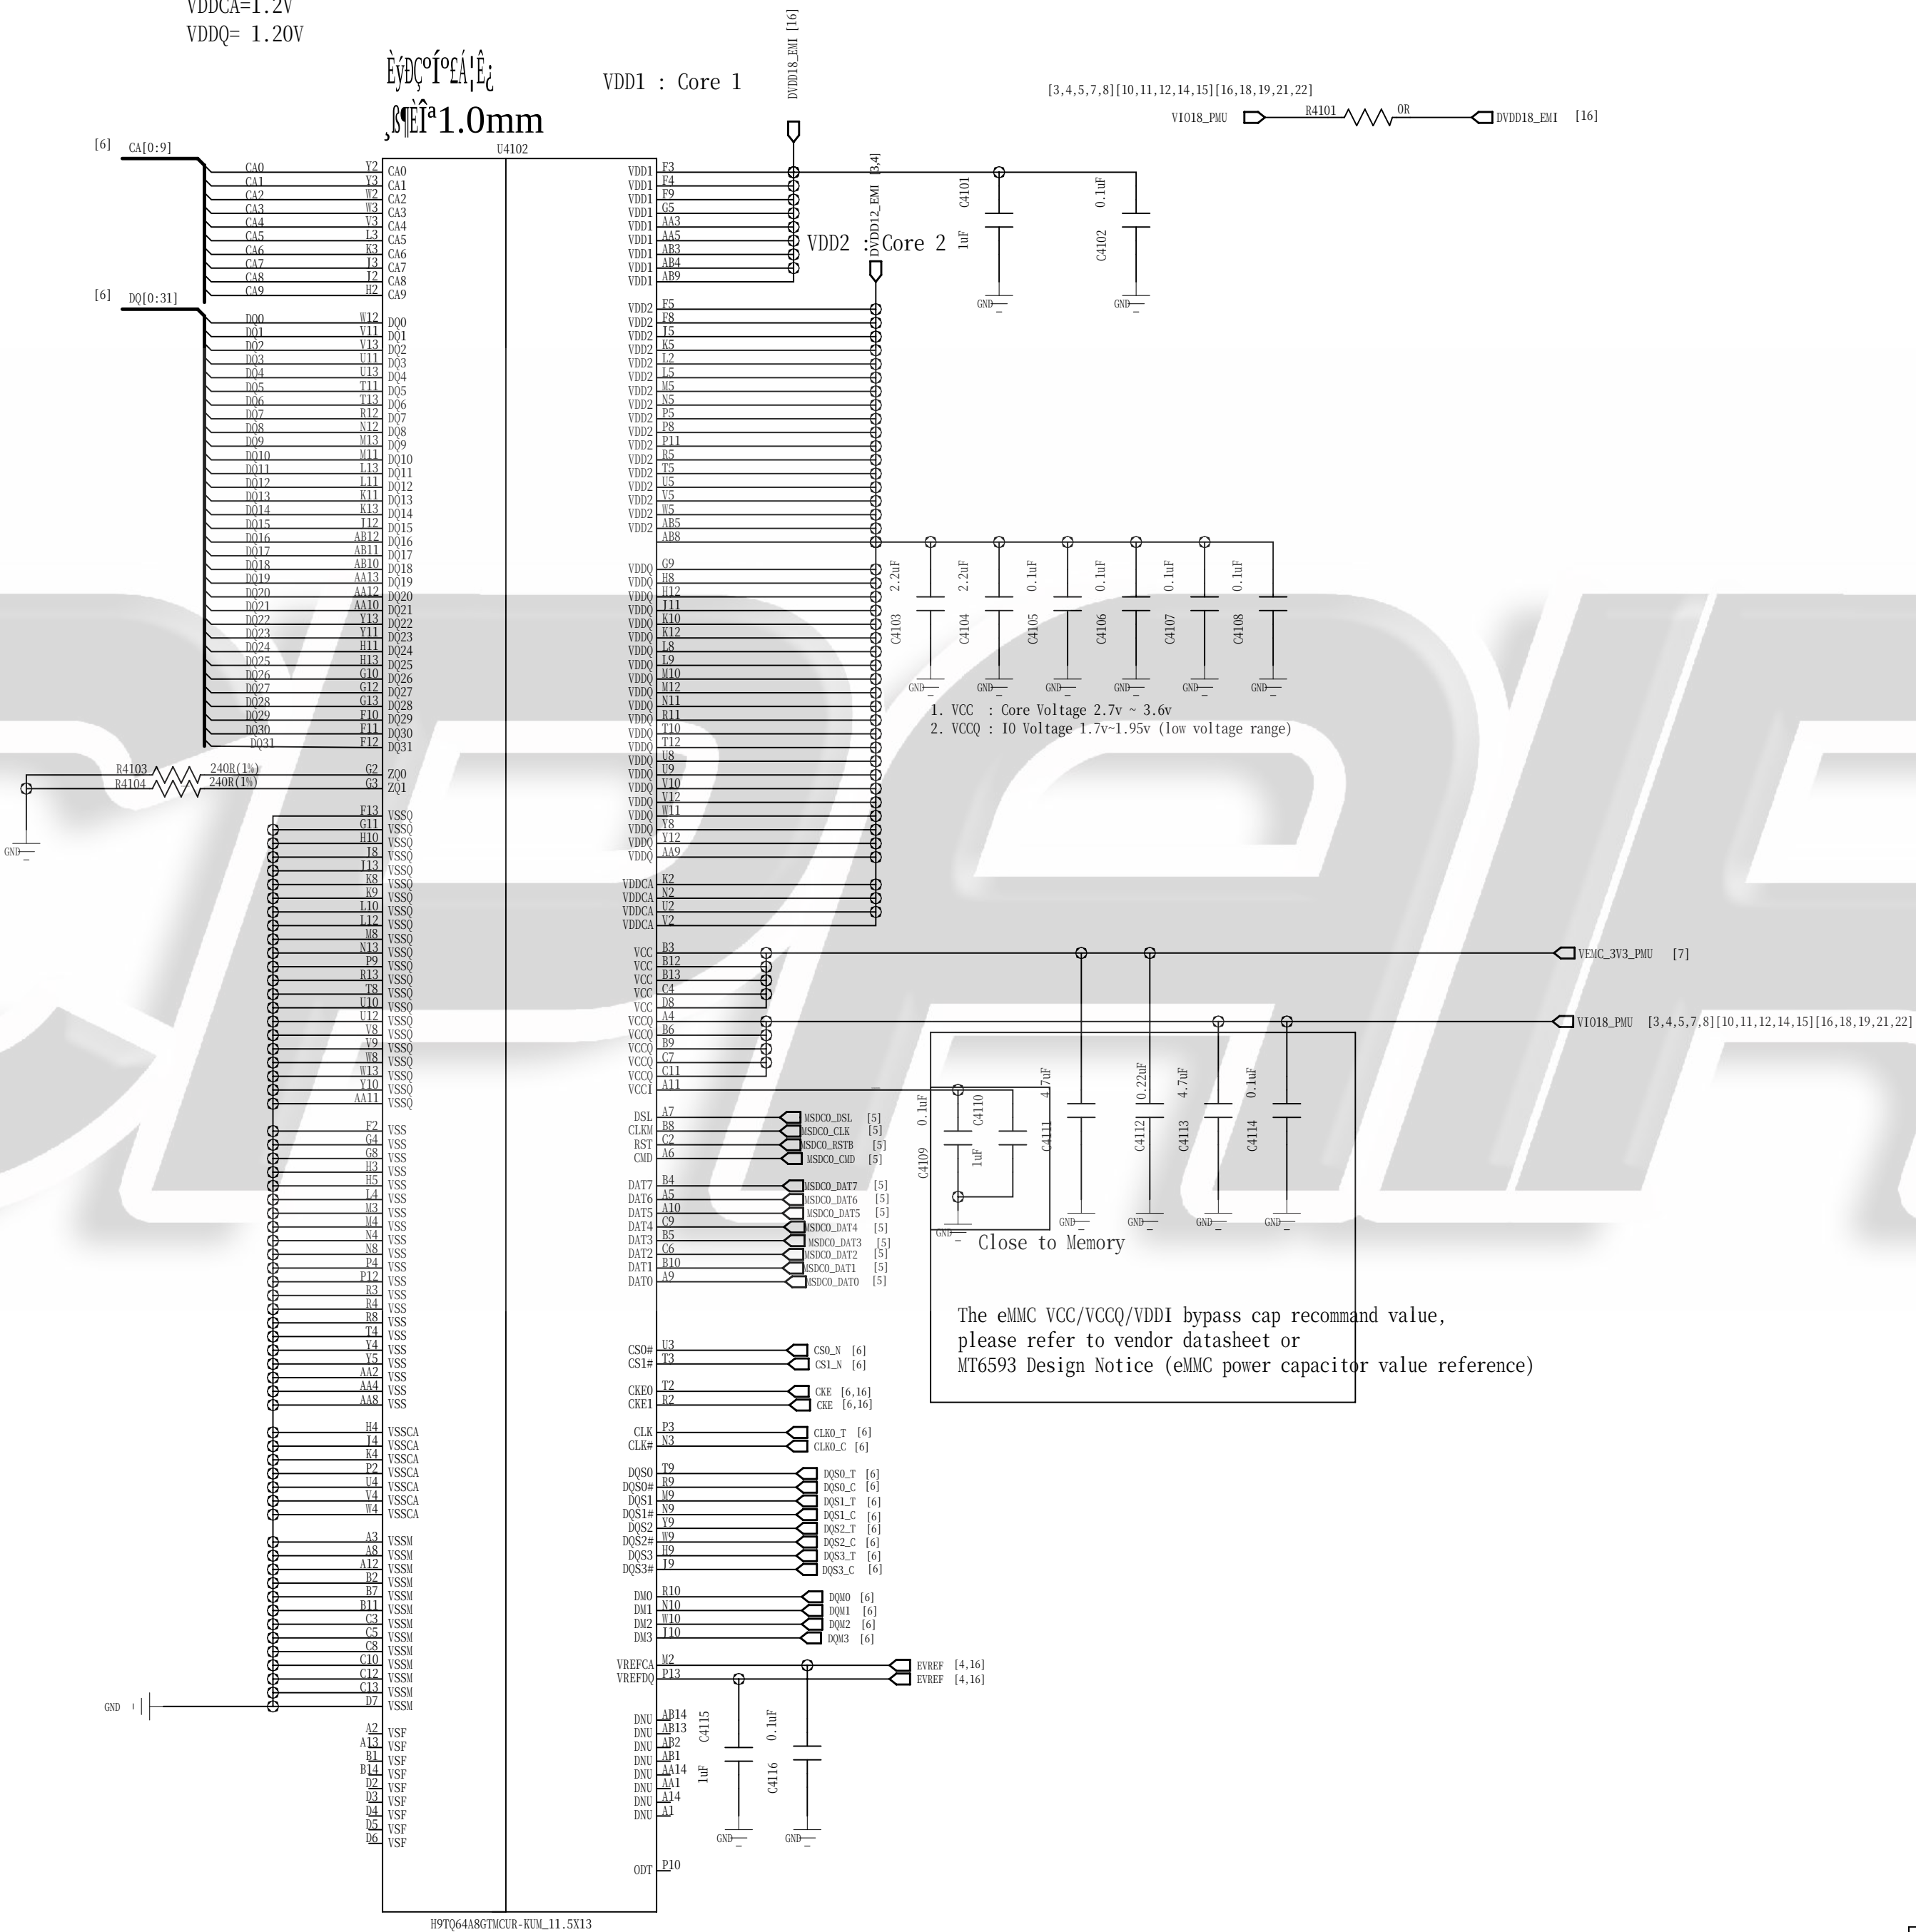

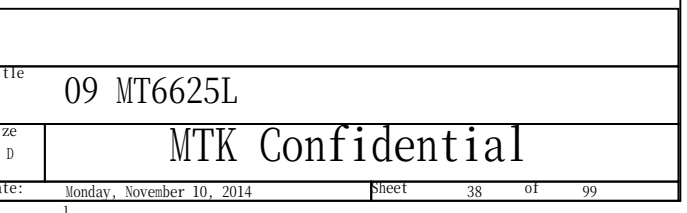

REVISION RECORD			
LTR	ECO NO:	APPROVED:	DATE:


Speaker

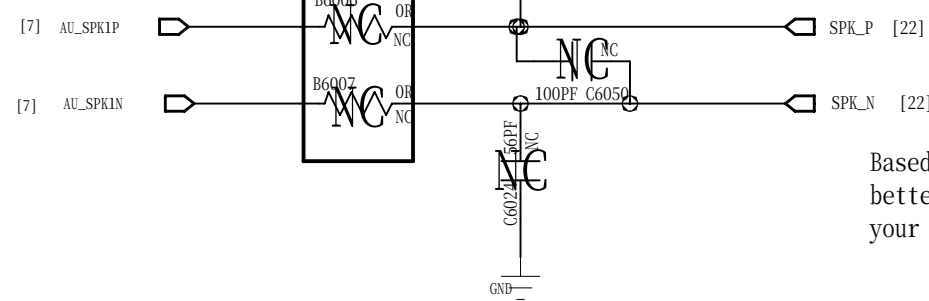

Based on your system level design , if better ESD performance is needed on your system.

Based on your system level design , if better desense performance is needed on your system.

Handset Microphone 1

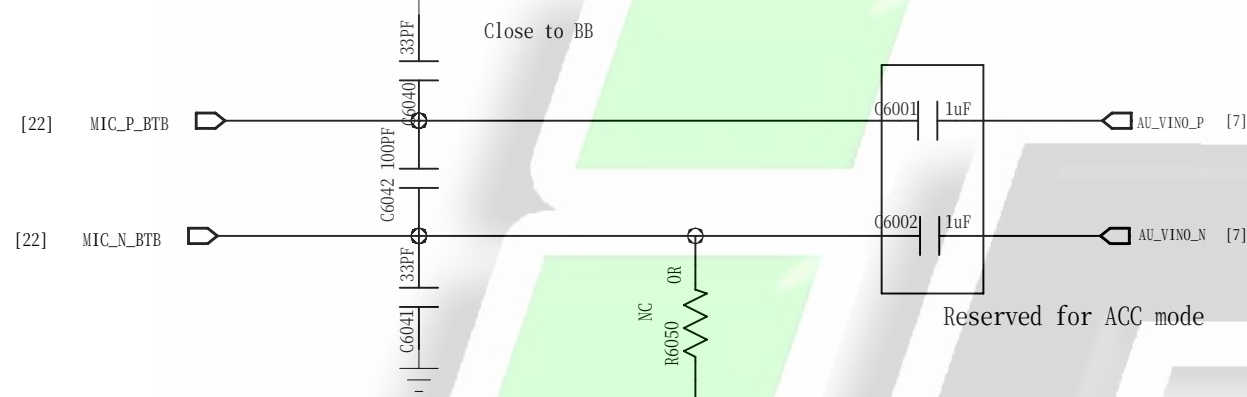


Reserved for ACC mode

Based on your system level design, if better audio performance is needed on your system, please reserve for ACC mode

Second MIC

Handset Microphone

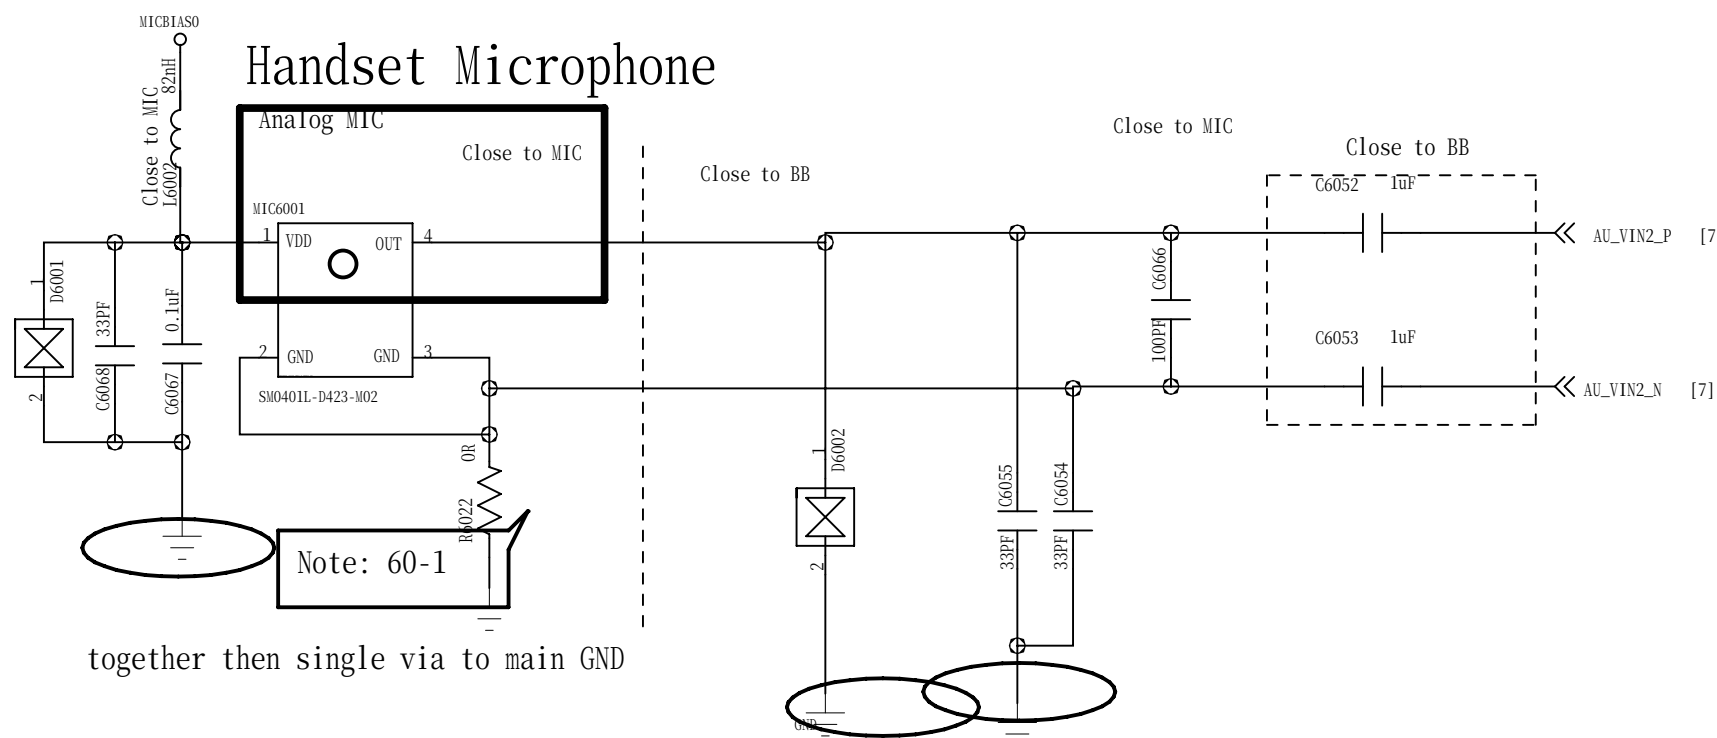

Close to MIC

Close to BB

Close to MIC


Close to BB

together then single via to main GND

Earphone Audio


Based on your system level design , if better Audio performance is needed on your system, please add 32ohm to audio path for performance enhance proposal (32ohm condition pop noise can improve 6dB)

BEAD6001 / BEAD6002 are for FM-desense tuning proposal

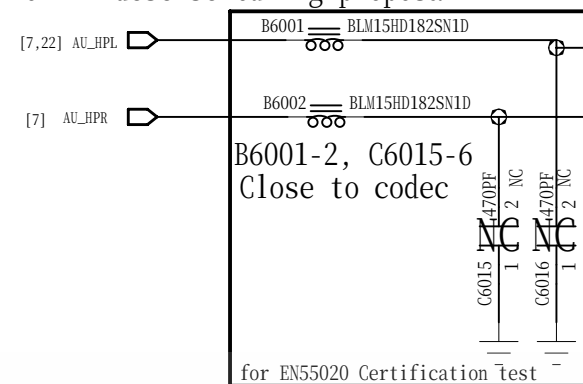


for ENS5020 Certification Test

Earphone MICPHONE

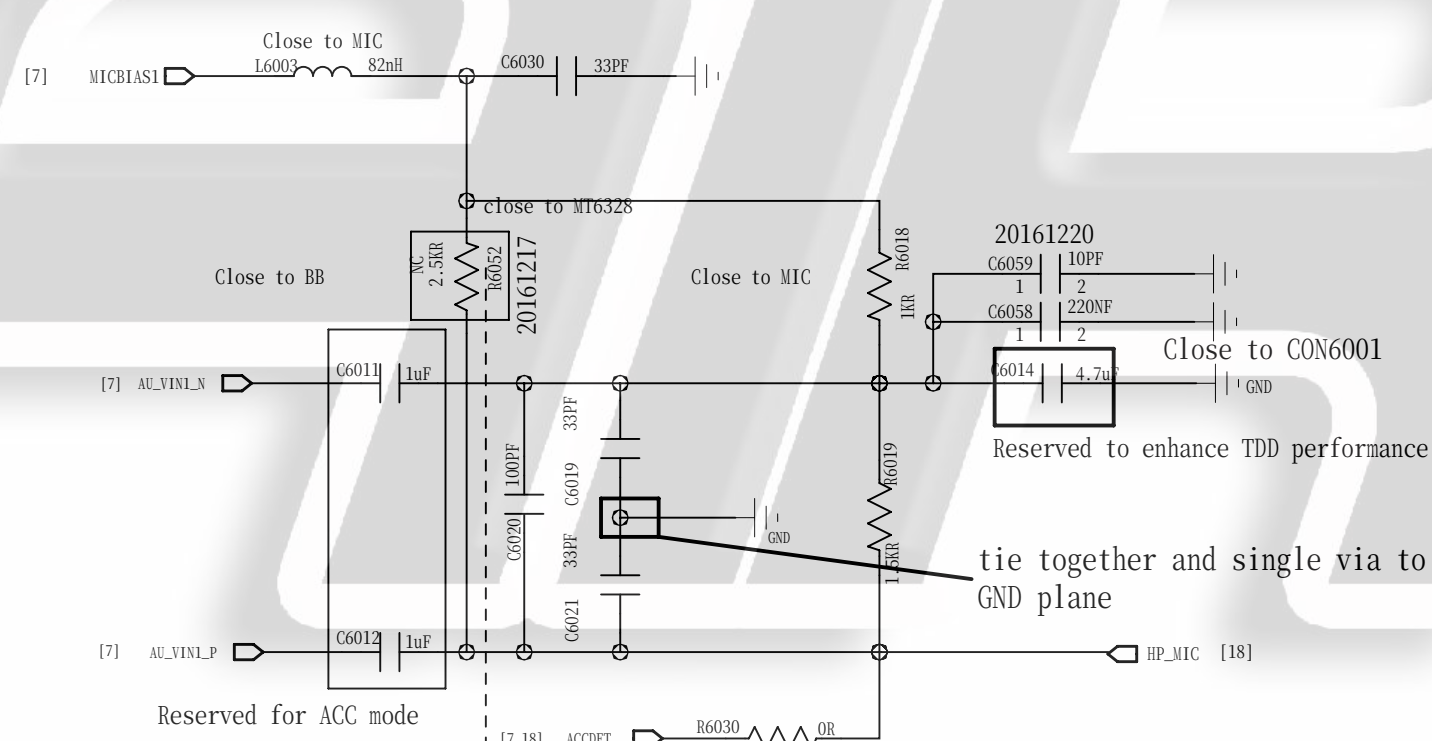

Receiver




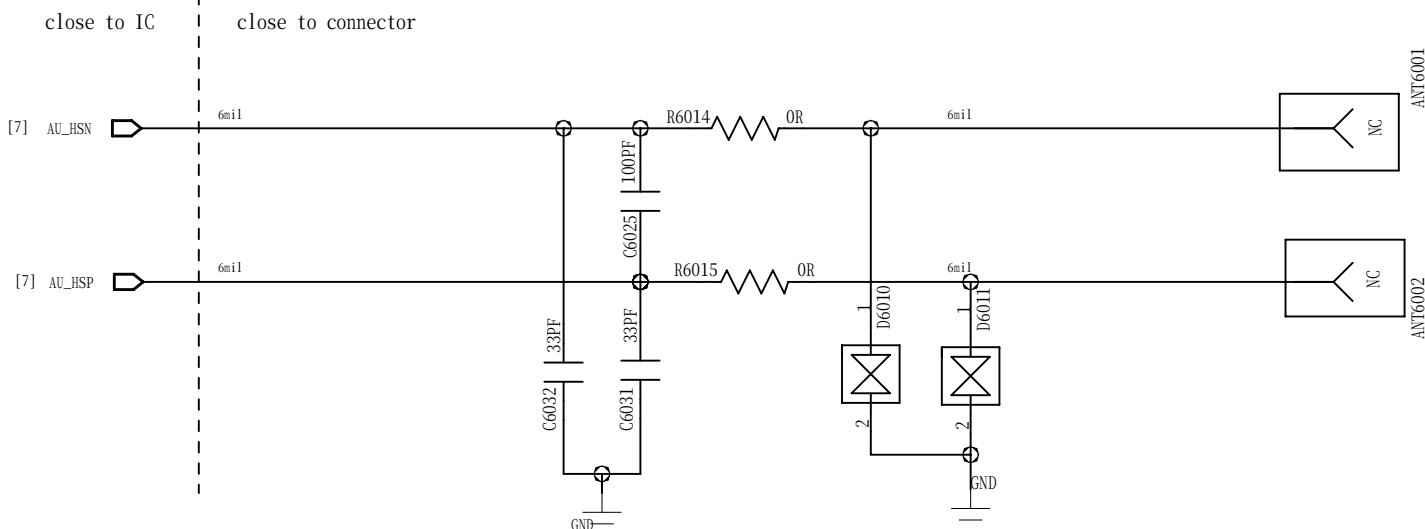


Based on your system level design , if better ESD performance is needed on your system.


DRAWN:	SUNHAO	DATED:	2016.01.21
CHECKED:	SUNHAO	DATED:	<Checked Date>
QUALITY CONTROL:	<QC By>	DATED:	<QC Date>
RELEASED:	<Released By>	DATED:	<Release Date>

COMPANY: WIND			
TITLE: E187			
CODE:	SIZE:	DRAWING NO:	REV:
<Code>	D	<Drawing Number>	<Revision>
SCALE: <Scale>		SHEET: 18# 23	

REVISION RECORD			
LTR	ECO NO:	APPROVED:	DATE:

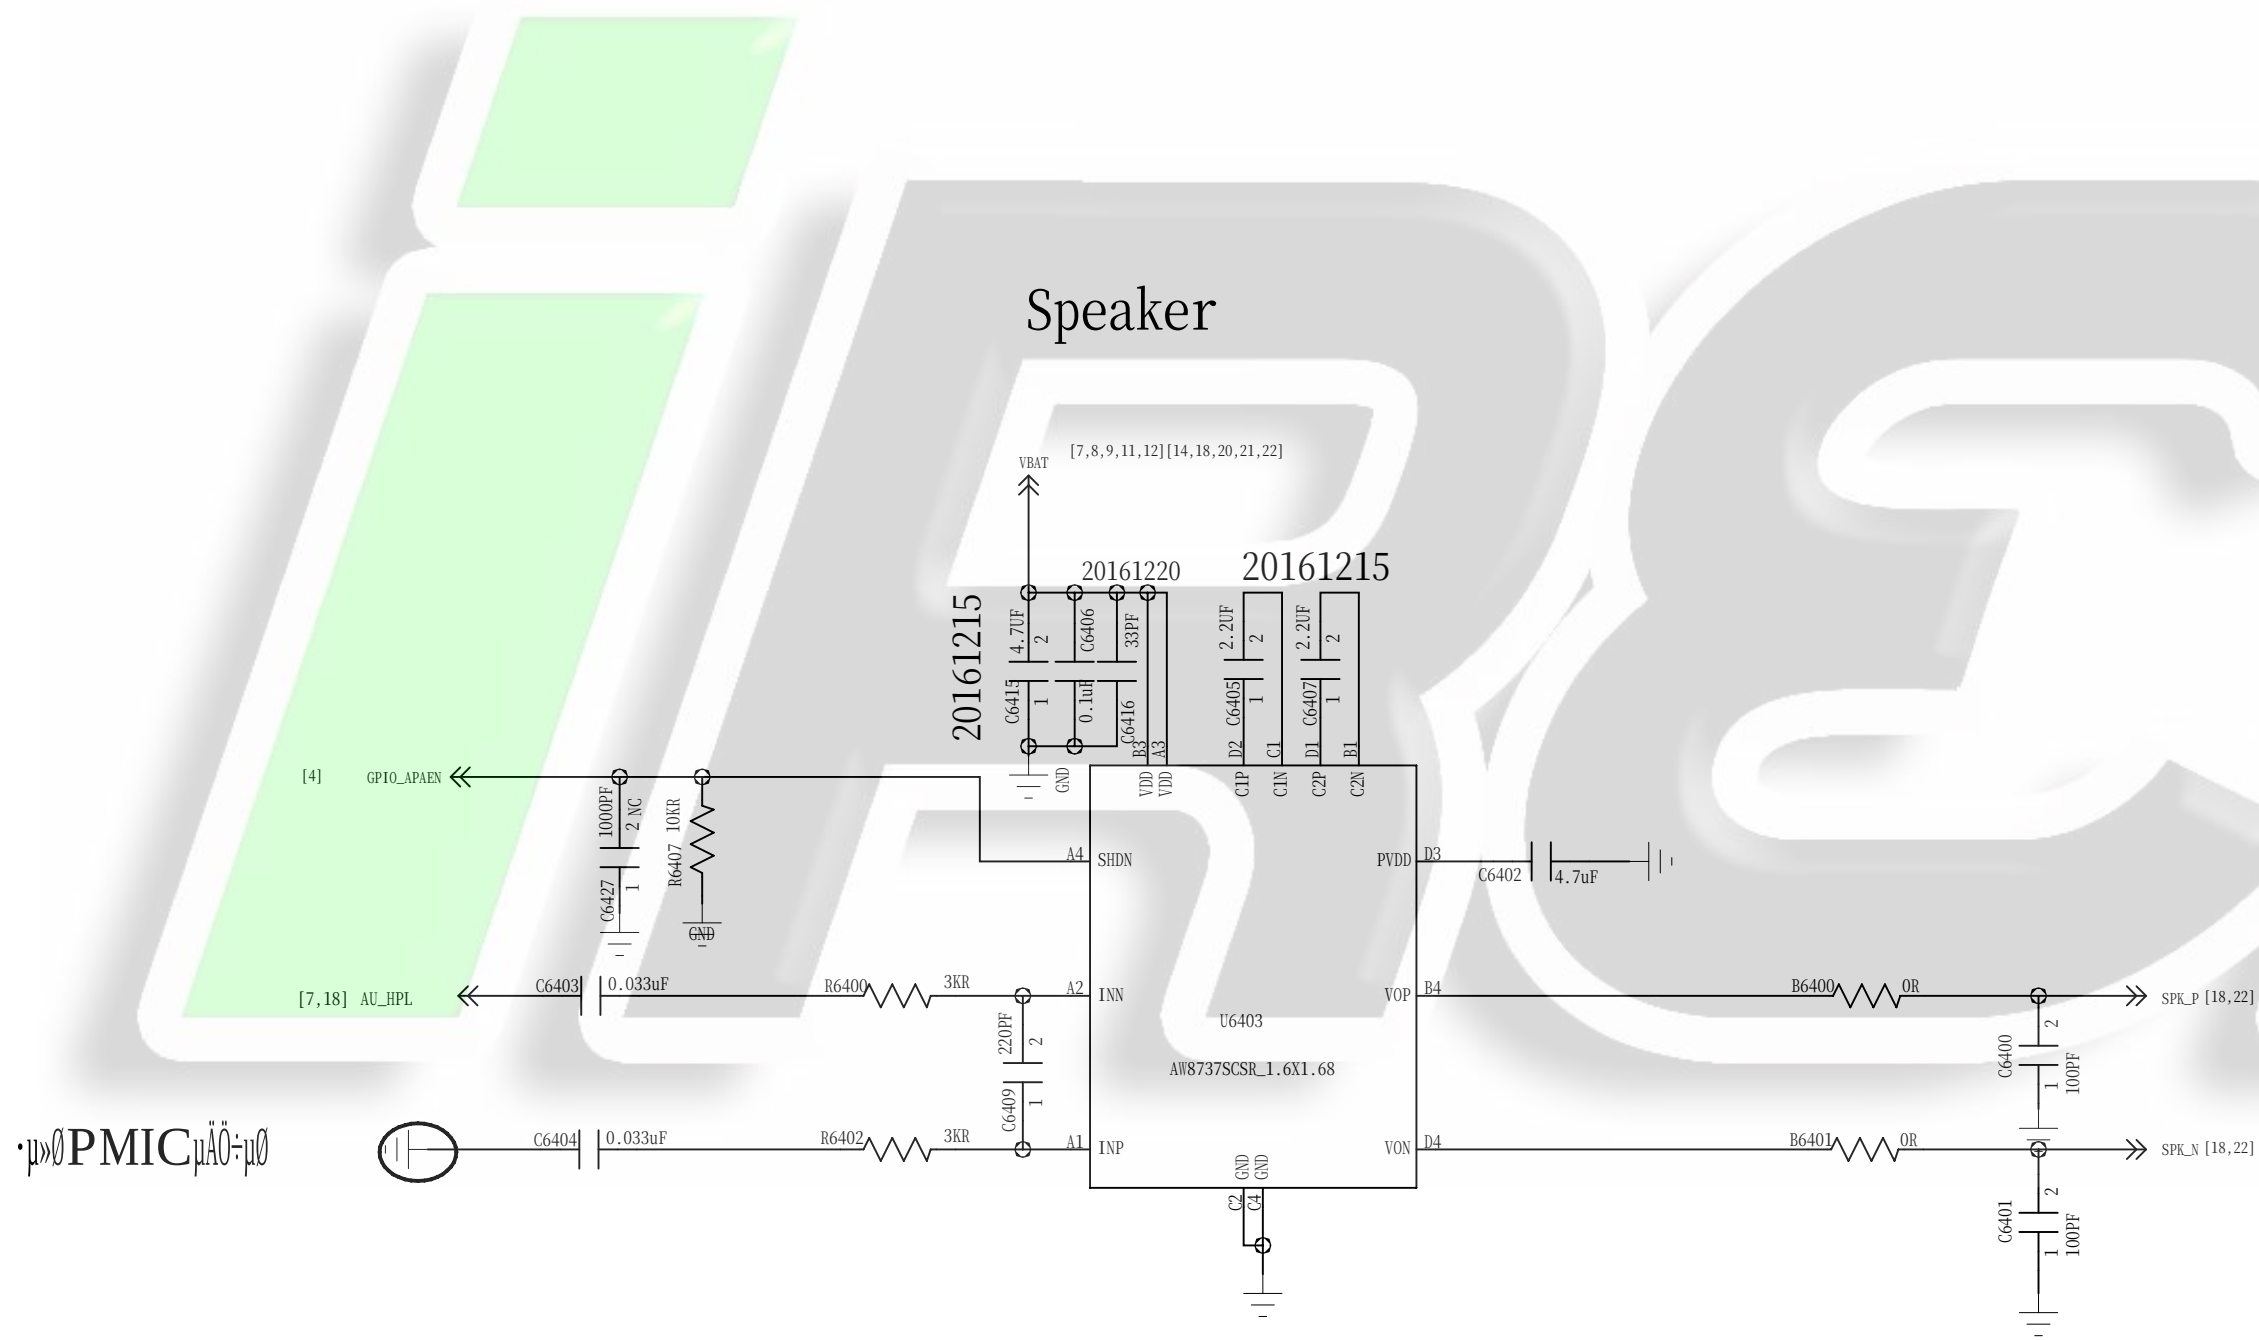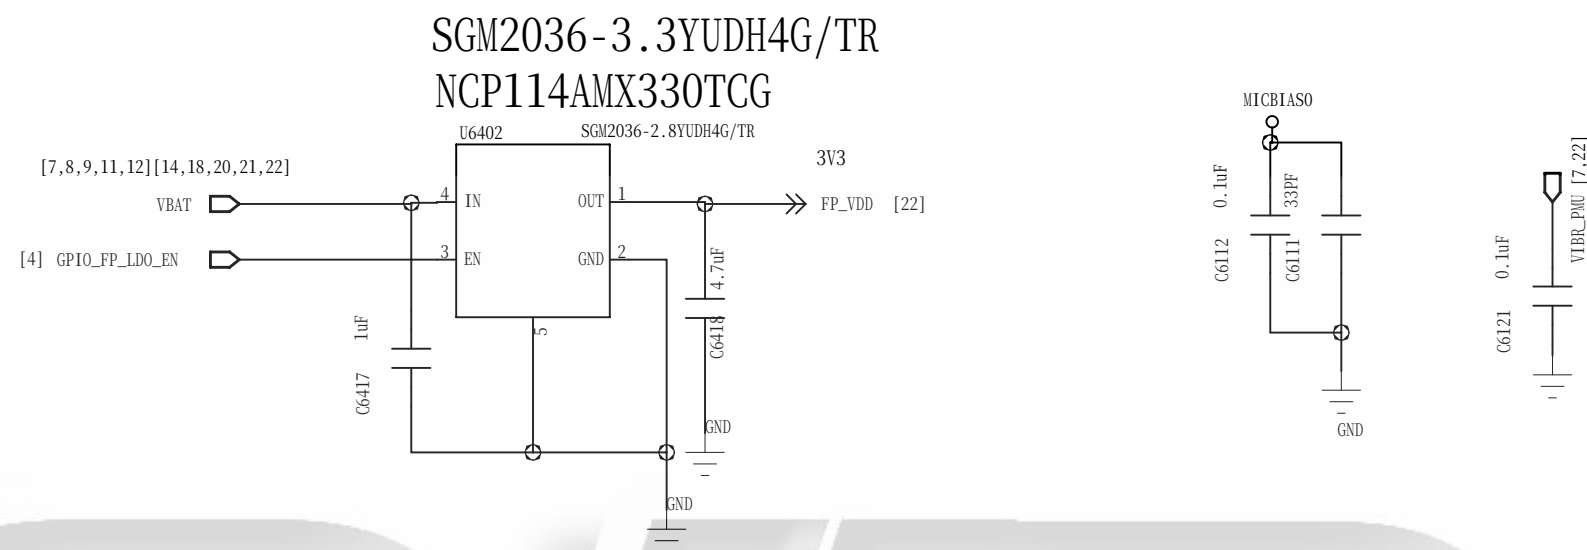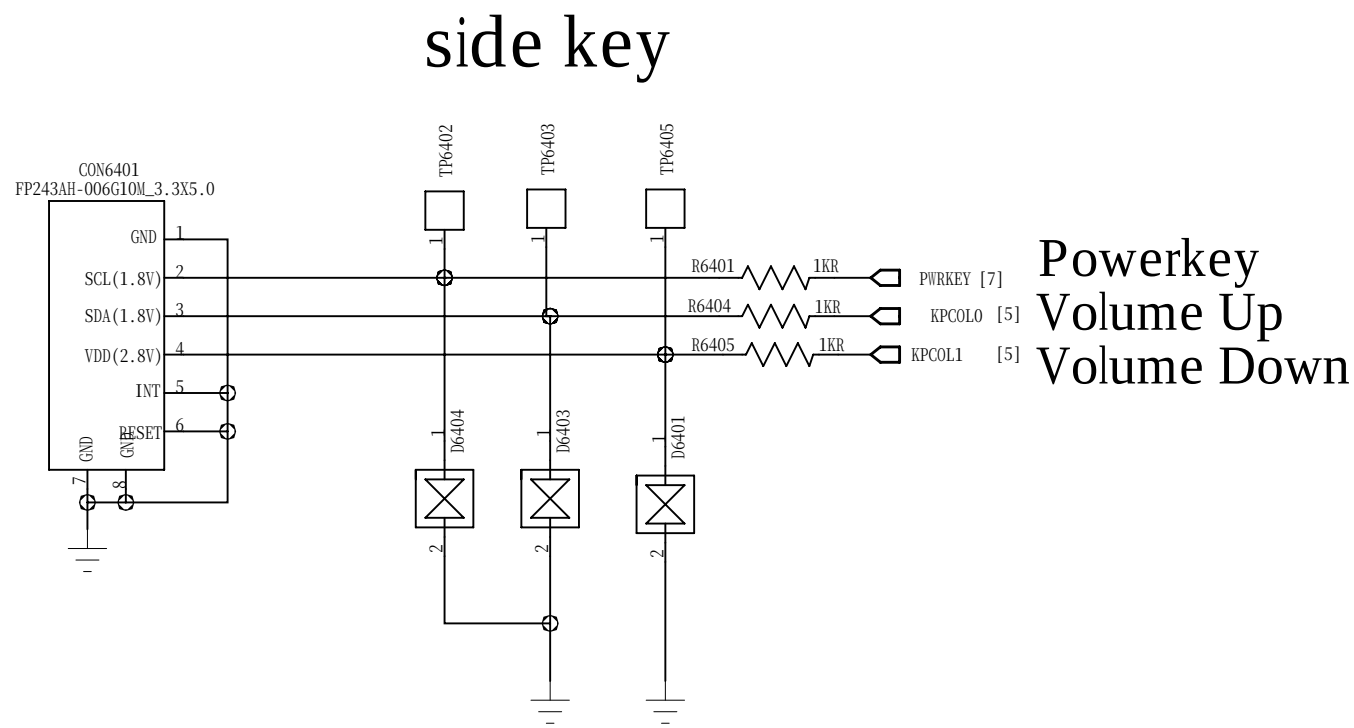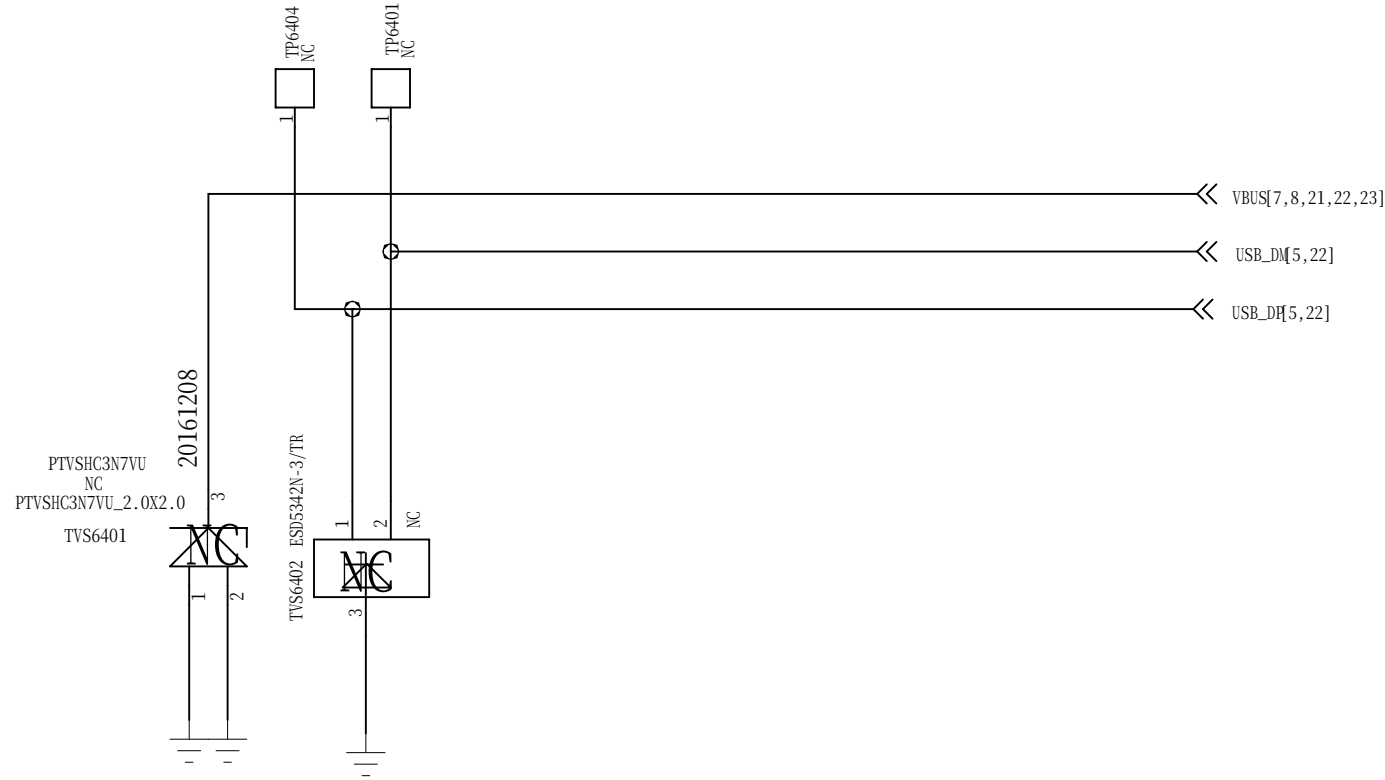

Fingerprint

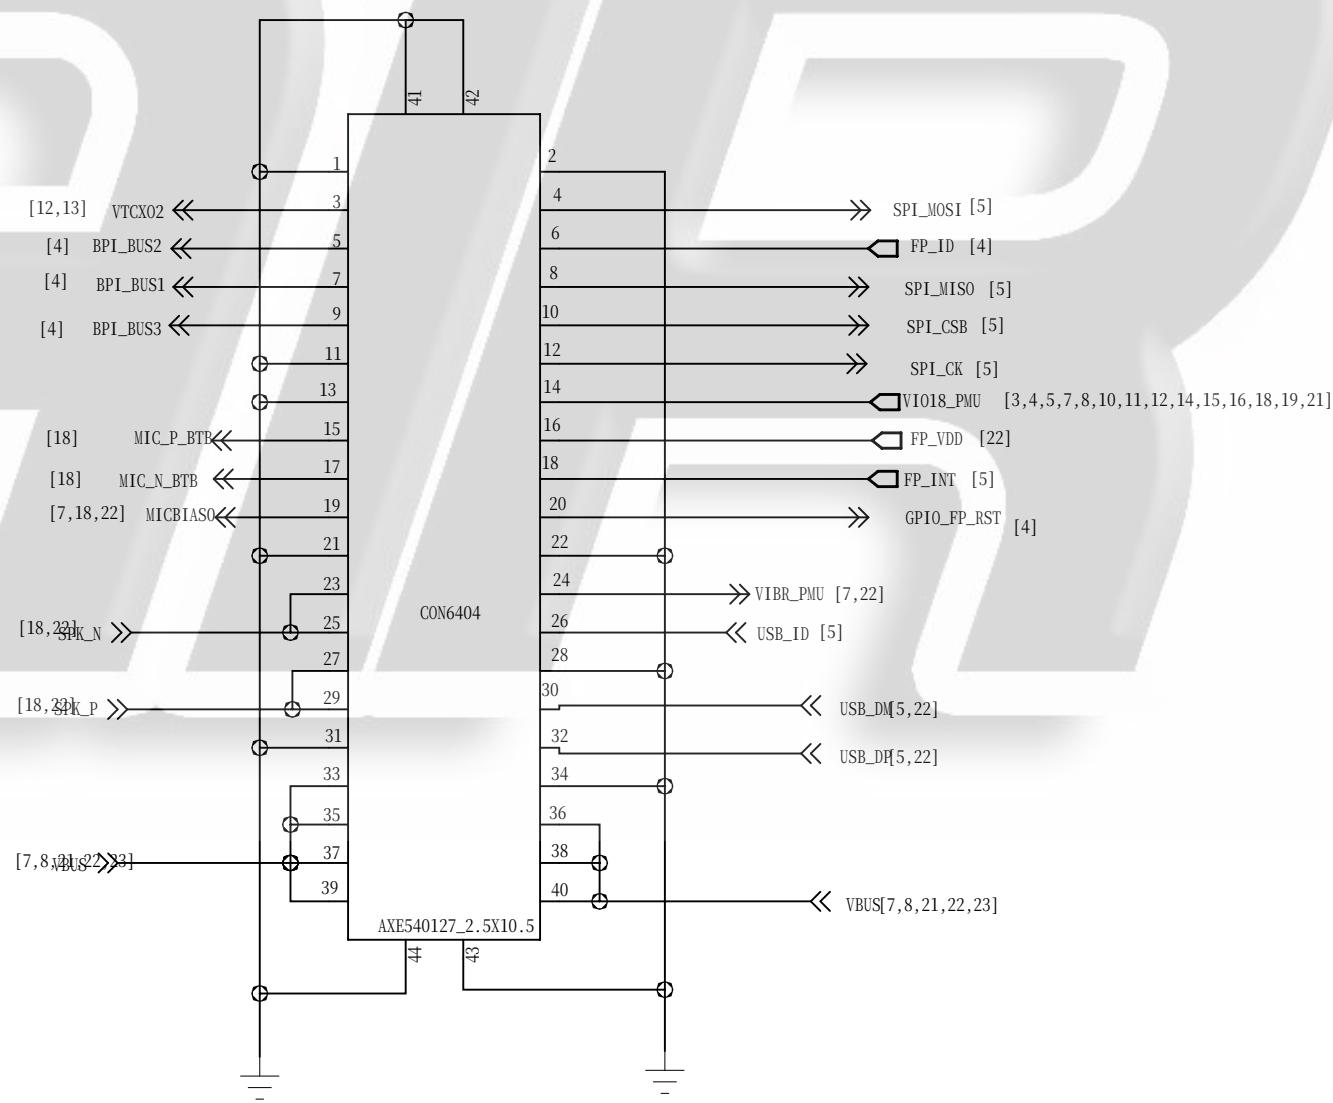


COMPANY: WIND			
TITLE: E187			
DRAWN: SUNHAO	DATED: 2016.01.21	CODE: <Code>	SIZE: D
CHECKED: SUNHAO	DATED: <Checked Date>	DRAWING NO: <Drawing Number>	REV: <Revision>
QUALITY CONTROL: <QC By>	DATED: <QC Date>	SCALE: <Scale>	
RELEASED: <Released By>	DATED: <Release Date>	SHEET: 22/ 23	


REVISION RECORD			
LTR	ECO NO:	APPROVED:	DATE:

UART只是测试不按照生产要求
开关机键电源键，USB按照生产要求摆放2.5mm

BOT面电池盖接地弹片，中间两个天线要求兼容0R到地。

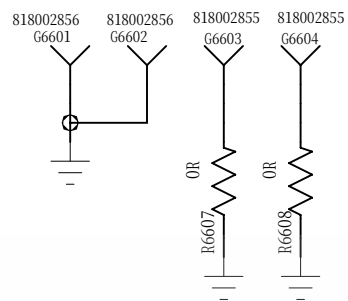


TEST POINTS

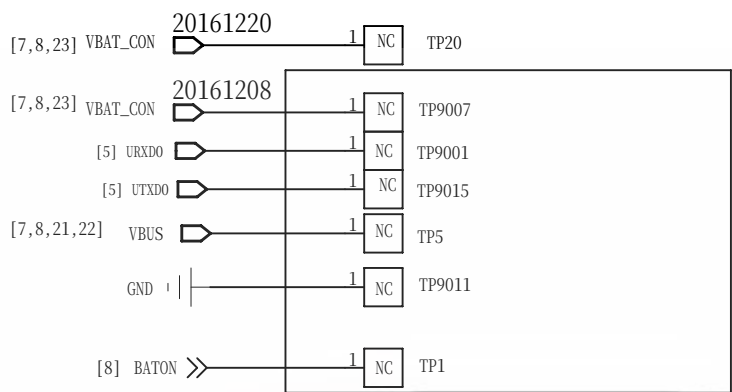


NC


TOP面前壳耳机旁边和两边的接地弹片

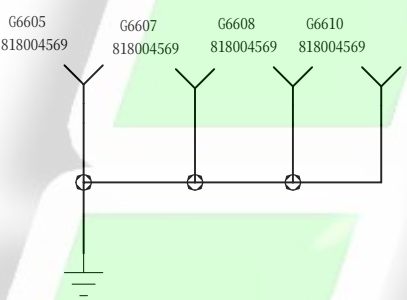

BOT面二合一卡座旁边的接地弹片

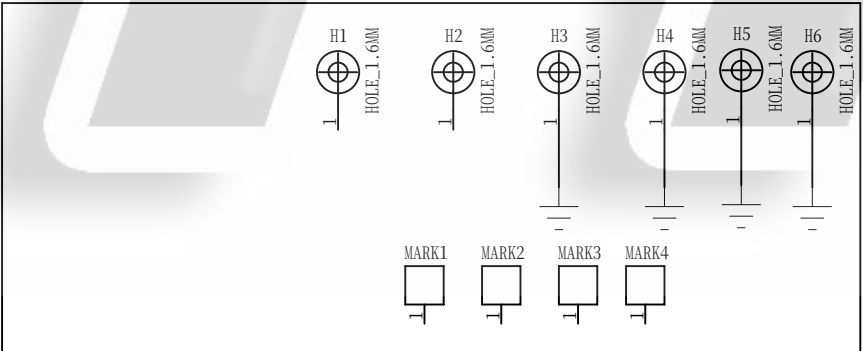

NC

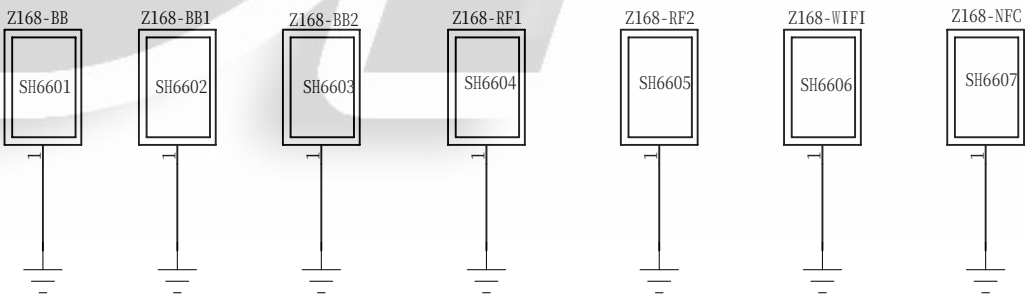

COMPANY: WIND			
TITLE: E187			
DRAWN: SUNHAO	DATED: 2016.01.21	CODE: <Code>	SIZE: D
CHECKED: SUNHAO	DATED: <Checked Date>	DRAFTING NO: <Drawing Number>	REV: <Revision>
QUALITY CONTROL: <QC By>	DATED: <QC Date>	SCALE: <Scale>	
RELEASED: <Released By>	DATED: <Release Date>	SHEET: 23# 23	

have checked